

PROFESSIONAL ENGINEERS

10009 GALLANT LANE
TAMPA, FLORIDA 33625
813-444-7037



ADVANCED ENGINEERING
CONSULTANTS LLC

JOB DESCRIPTION

THE PURPOSE OF THIS DESIGN PACKAGE IS FOR
THE REINFORCEMENT OF EXISTING WARPED ROOF TRUSSES

BISHOP RD TRUSS REPAIR
SINGLE FAMILY RESIDENTIAL

2187 BISHOP RD,
SPRING HILL, FL 34608

CLASSIFICATION OF WORK

THIS DESIGN'S CLASSIFICATION OF WORK IS A "REPAIR" AS DEFINED IN 2023
FLORIDA BUILDING CODE - EXISTING, 8TH EDITION, CHAPTER 4 SECTION 401.

AUTHORITY HAVING JURISDICTION

HERNANDO COUNTY

PROJECT BISHOP RD
TRUSS REINF.

ADDRESS
2187 BISHOP RD,
SPRING HILL, FL 34608

FOR REVIEW

ADVANCED ENGINEERING PROJECT NUMBER
26056

This drawing is the property of Advanced
Engineering and is not to be reproduced or copied
in whole or in part.



ADVANCED
ENGINEERING
CONSULTANTS
(813) 444-7037
www.Advanced-Engineers.com
10009 Gallant Lane
Tampa, FL 33625

ENGINEER OF RECORD: PETER D. MILLER, P.E.
FLORIDA P.E. LICENSE NO.: 104758
FLORIDA REGISTRY NO.: 28038
NOT APPROVED FOR PERMIT UNLESS
DULY SIGNED AND SEALED BY ENGINEER

Digitally
signed by
Peter D Miller
Date:
2026.07.22
10:53:12 EDT

PETER D. MILLER, STATE OF FLORIDA,
PROFESSIONAL ENGINEER, LICENSE NO. 104758
THIS ITEM HAS BEEN DIGITALLY SIGNED AND SEALED BY
PETER D. MILLER ON THE DATE INDICATED HERE.
SIGNATURE MUST BE VERIFIED ON ANY ELECTRONIC COPIES.
PER RULE 61G15-23.004 (3)(D)(2) WHEN A DIGITALLY CREATED
SEAL IS NOT USED AND PARAGRAPH (E) "A DIGITAL SIGNATURE
APPLIED TO AN ITEM IN ELECTRONIC FORM SHALL HAVE THE
SAME FORCE AND EFFECT AS SIGNING ALL OF THE INDIVIDUAL
SHEETS OR PAGES CONTAINED WITHIN THAT ITEM UNLESS
OTHERWISE LIMITED AS SPECIFIED IN SUBSECTION
61G15-30.003(3), F.A.C."

THESE PLANS WERE PREPARED IN ACCORDANCE TO F.S.
CHAPTER 471 AND APPLICABLE FLORIDA BUILDING CODE
8TH EDITION, 2023. ANY SERVICES OF AN
ARCHITECTURAL NATURE REFLECTED IN THIS PLAN ARE
BEING PERFORMED AS PURELY INCIDENTAL TO MY
ENGINEERING PRACTICE PURSUANT TO SECTION
471.00(3), F.S. THIS DESIGN IS SITE SPECIFIC AND MAY
NOT BE USED AT OTHER LOCATIONS WITHOUT THE
CONSENT OF ADVANCED ENGINEERING CONSULTANTS
LLC. THIS DOCUMENT AND ALL REPORTS, DRAWINGS,
SPECIFICATIONS AND COMPUTER FILES, PREPARED BY
ADVANCED ENGINEERING CONSULTANTS LLC, SHALL
REMAIN THE PROPERTY OF ADVANCED ENGINEERING
CONSULTANTS LLC, AND SHALL NOT BE REPRODUCED,
IN PART OR WHOLE, WITHOUT THE EXPRESSED,
WRITTEN, CONSENT OF ADVANCED ENGINEERING
CONSULTANTS LLC. ADVANCED ENGINEERING
CONSULTANTS LLC SHALL RETAIN ALL COMMON LAW,
STATUTORY AND OTHER RESERVED RIGHTS, INCLUDING
THE COPYRIGHT THERE TO.

DRAWINGS

STRUCTURAL SET

REVISIONS
No. Date Description

PLANS TO BE PRINTED IN COLOR

DRAWN & DESIGNED BY
CB

CHECKED BY
PM, MH

INITIAL RELEASE DATE
2026-07-22

SHEET TITLE

COVER

PLANS ARE TO BE PRINTED IN COLOR


SCALE
AS NOTED

SHEET NUMBER

G-1

PLANS TO BE PRINTED IN COLOR


LOCATION MAP

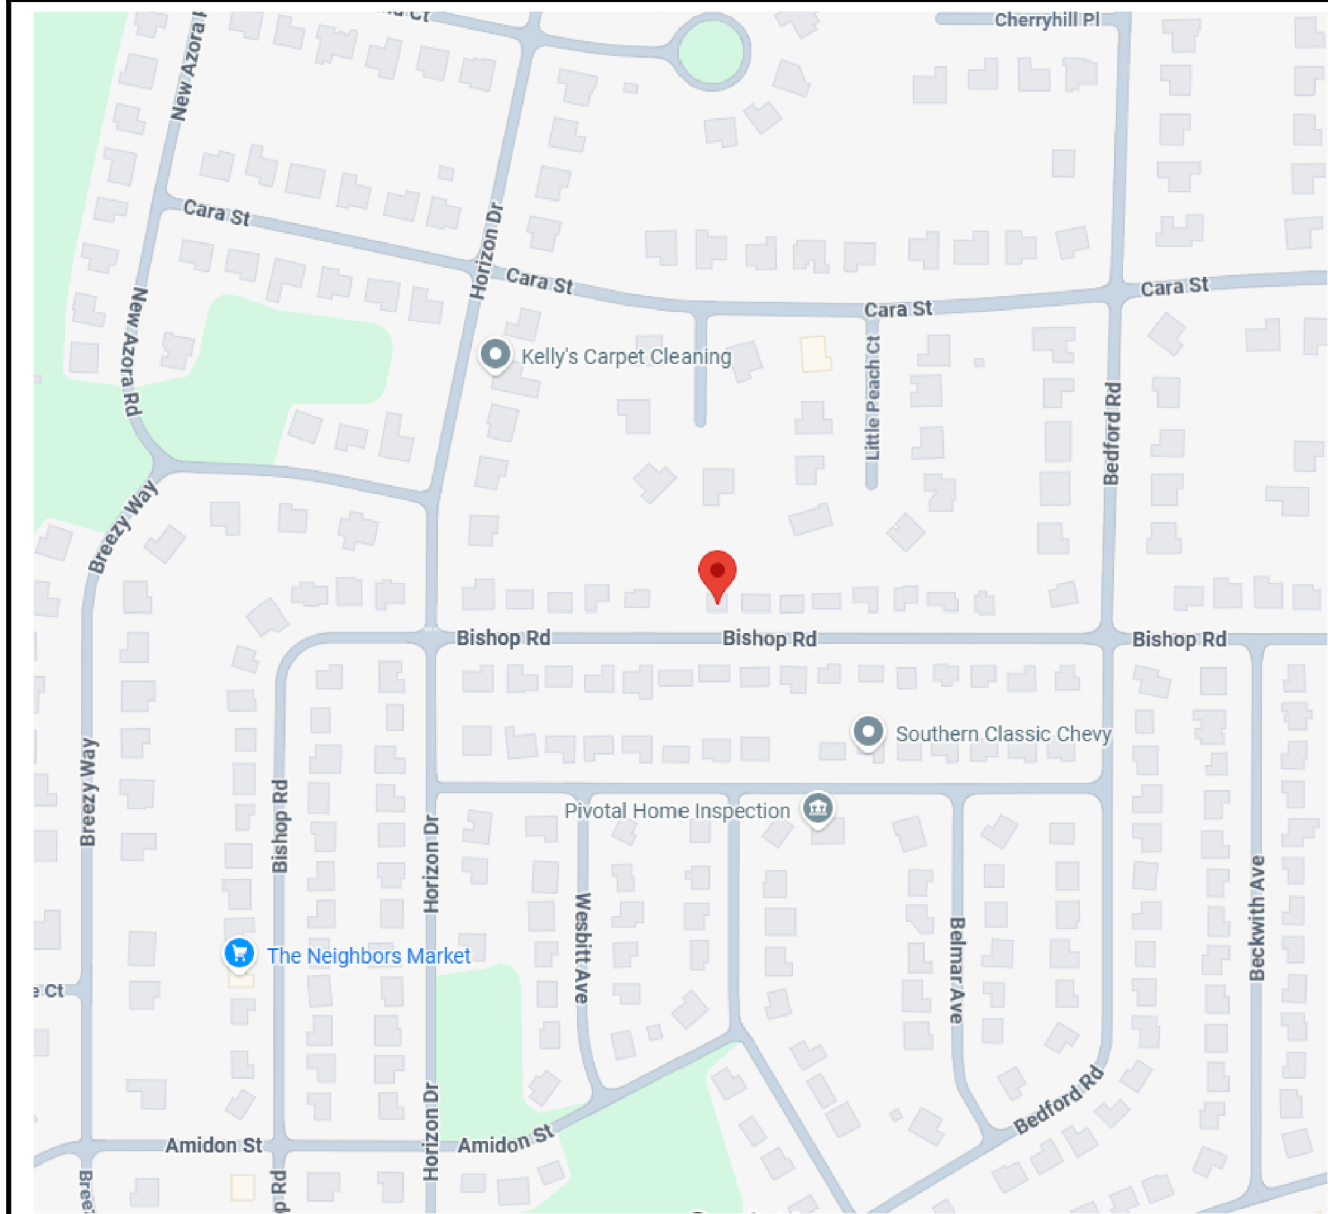

FRONT ELEVATION



VICINITY MAP

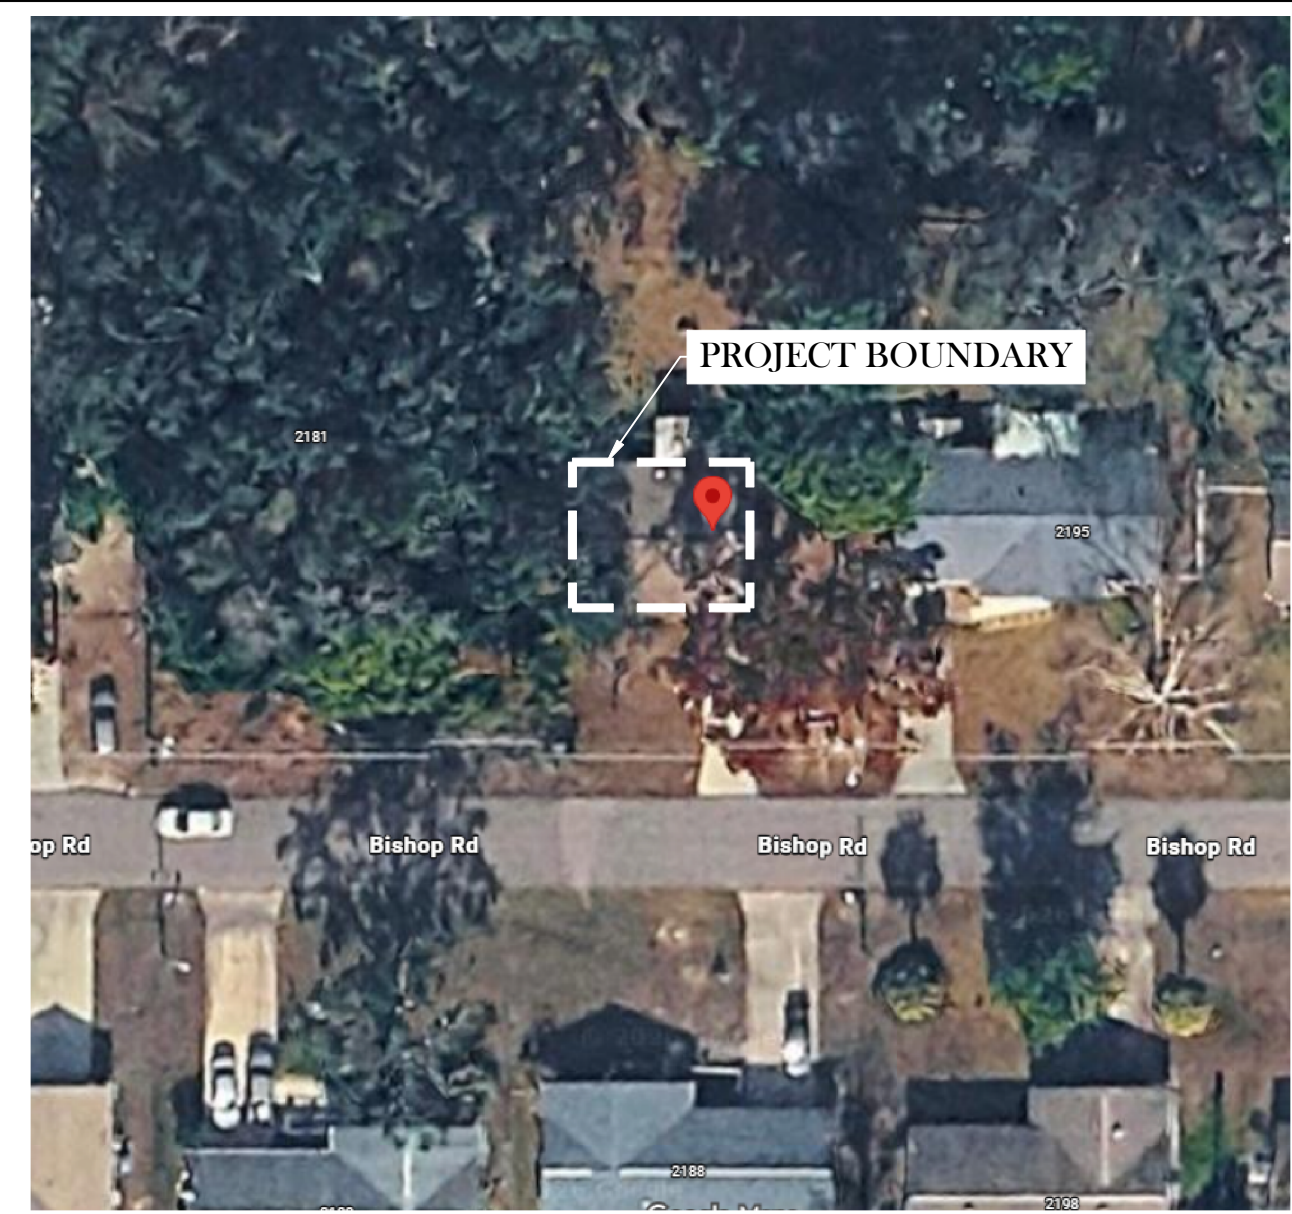

APPLIED CODES

- FLORIDA BUILDING CODE - RESIDENTIAL - 8TH EDITION (2023)


ABBREVIATIONS

ABV	ABOVE	MECH	MECHANICAL
ADJ	ADJUSTABLE	MFR	MANUFACTURER
AFR	ABOVE FINISH FLOOR	MIN	MINIMUM
ALT	ALTERNATE	MTL	METAL
ALLM	ALUMINUM	NIC	NOT IN CONTRACT
BLDG	BUILDING	NIS	NOT IN SCOPE
BOT	BOTTOM	NO	NUMBER
B.O.	BOTTOM OF	NOM	NOMINAL
CJ	CONTROL JOINT	NTS	NOT TO SCALE
CLG	CEILING	OC	ON CENTER
CLR	CLEAR	OD	OUTSIDE DIAMETER
CMU	CONCRETE MASONRY UNIT	OOS	OUT OF SCOPE
CONC	CONCRETE	PLAM	PLASTIC LAMINATE
COL	COLUMN	PT	PRESSURE TREATED
PTD	PAINTED	REF	REFERENCE
DET.	DETAIL	REIN	REINFORCING
DIM	DIMENSION	REQ	REQUIRED
DN	DOWN	RM	ROOM
DWG(S)	DRAWING(S)	RO	ROUGH OPENING
EA	EACH	RV	ROOF VENT
EF	EXHAUST FAN	SCH	SCHEDULE
EJ	EXPANSION JOINT	SEC	SECTION
ELEC	ELECTRICAL	SF	SQUARE FOOT
ELV	ELEVATION	SGD	SLIDING GLASS DOOR
ELV	ELEVATOR	SIM	SIMILAR
E.O.R.	ENGINEER OF RECORD	SPEC	SPECIFICATION
EQ	EQUAL	SQ FT	SQUARE FOOT
EQUIP	EQUIPMENT	SS	STAINLESS STEEL
ETR	EXISTING TO REMAIN	STD	STANDARD
EW	ELECTRIC WATER COOLER	STL	STEEL
EXP	EXPANSION	STOR	STORAGE
EX	EXISTING	STRUCT	STRUCTURAL
EXT	EXTERIOR	T&G	TONGUE & GROOVE
FD	FLOOR DRAIN	TEMP	TEMPORARY
FE	FIRE EXTINGUISHER	THK	THICKNESS
FEC	FIRE EXTINGUISHER CABINET	TOD	TOP OF DOOR
FF	FINISHED FLOOR	TOM	TOP OF MASONRY
FL#	FLORIDA PRODUCT APPROVAL	TOS	TOP OF STEEL
FT	FOOT OR FEET	TOW	TOP OF WINDOW
GA	GAUGE	TOWA	TOP OF WALL
GYP	GYPNUM	TYP	TYPICAL
HT	HEIGHT	UNO	UNLESS NOTED OTHERWISE
HDRW	HARDWARE	VAR	VARIABLE
HORIZ	HORIZONTAL	VERT	VERTICAL
ID	INSIDE DIAMETER	VIF	VERIFY IN FIELD
INS	INSULATION	VPAB	VAPOR PERMEABLE AIR BARRIER
LAM	LAMINATED	W/	WITH
MATL	MATERIAL	WD	WOOD
MAX	MAXIMUM	WVF	WELDED WIRE FABRIC
MB	MODIFIED BITUMEN		

INDEX OF DRAWINGS

GENERAL	REV	DATE
G-1 COVER PAGE		
S-1 STRUCTURAL NOTES & FRAMING PLAN		
S-2 STRUCTURAL DETAILS		

SYMBOLS

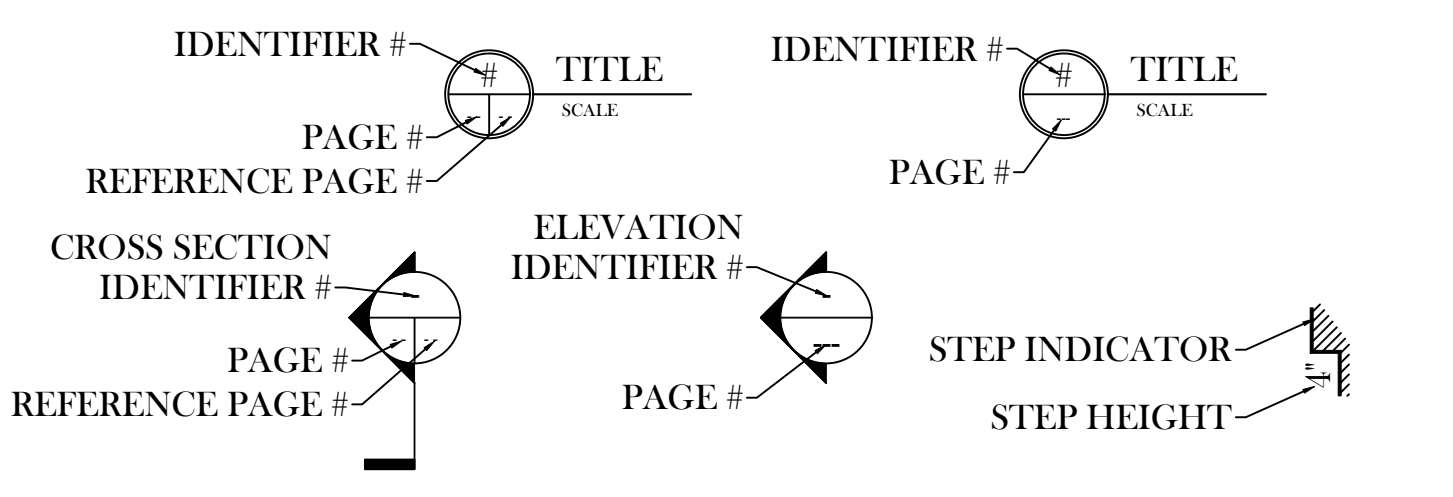

STRUCTURAL CERTIFICATION STATEMENT AND DESIGN CRITERIA

TO THE BEST OF MY KNOWLEDGE THESE PLANS COMPLY WITH THE FLORIDA
BUILDING CODE - RESIDENTIAL 2023 AND THE LOAD REQUIREMENTS OF ASCE 7.

FLORIDA PRODUCT APPROVALS PER FLOOR PLAN
AND SHALL COMPLY WITH THE MINIMUM
ALLOWABLE WIND PRESSURES ON THIS SHEET.

DEFLECTION CRITERIA PER FBC, TABLE R301.7
FLOOR/CEILINGS (LL):
RAFTERS W/ SLOPE > 3:12 (LL):
ALL OTHER:
SUPER IMPOSED LOAD DESIGNS:
ROOF:
LL = 20 PSF


SUMMARY
RISK CATEGORY:
ULTIMATE WIND SPEED:
NOMINAL WIND SPEED:
EXPOSURE CATEGORY:
BUILDING LENGTH:
BUILDING WIDTH:
EXISTING MEAN ROOF HEIGHT:
ROOF SLOPE:
ROOF TYPE:
ENCLOSURE CLASSIFICATION:
INTERNAL PRESSURE COEF.

(NOTE THAT COMPONENT AND CLADDING LOADS
VARY AS A FUNCTION OF THE COMPONENT SIZE)

COMPONENT AND CLADDING DESIGN									
WIND PRESSURES (PSF)									
ROOF SURFACE PRESSURES									
Area	2 sf	10 sf	20 sf	50 sf	75 sf	100 sf	200 sf	250 sf	
Negative Zone 1 & 2e	-31.6	-31.6	-31.6	-19.2	-13.7	-10.0	-10.0	-10.0	
Negative Zone 2e, 2e & 2e	-46.1	-46.1	-39.9	-31.6	-28.0	-24.4	-19.1	-17.1	
Negative Zone 3r	-54.8	-54.8	-46.9	-36.6	-32.0	-28.7	-28.7	-28.7	
Positive All Zones	12.8	10.4	10.0	10.0	10.0	10.0	10.0	10.0	
Overhang Zone 1 & 2e	-36.2	-36.2	-36.2	-28.0	-24.3	-21.7	-21.7	-21.7	
Overhang Zone 2e & 2r	-50.7	-50.7	-46.1	-39.9	-37.1	-35.2	-30.5	-29.0	
Overhang Zone 3e	-59.4	-59.4	-51.3	-40.6	-35.8	-32.5	-24.4	-21.7	
Overhang Zone 3r	-68.1	-68.1	-57.7	-43.8	-37.7	-33.3	-33.3	-33.3	


NOTES:
1) TABLE PRESSURES ARE FOR THE SQUARE FOOT (SF) TRIBUTARY AREA SHOWN. FOR OTHER TRIBUTARY AREAS,
LINEARLY INTERPOLATE BETWEEN VALUES SHOWN ABOVE.
2) POSITIVE PRESSURES ACT TOWARD THE BUILDING. NEGATIVE PRESSURES ACT AWAY FROM THE BUILDING.
3) SEE DIAGRAMS FOR LOCATION OF ZONES.
4) PRESSURES SHOWN ARE NOMINAL PRESSURES, DIVIDE BY 0.6 FOR ULTIMATE PRESSURES

FOR SI: 1 foot= 304.8mm, 1 degree = 0.0175 rad
FIGURE R301.2(7) COMPONENT AND CLADDING PRESSURE ZONES

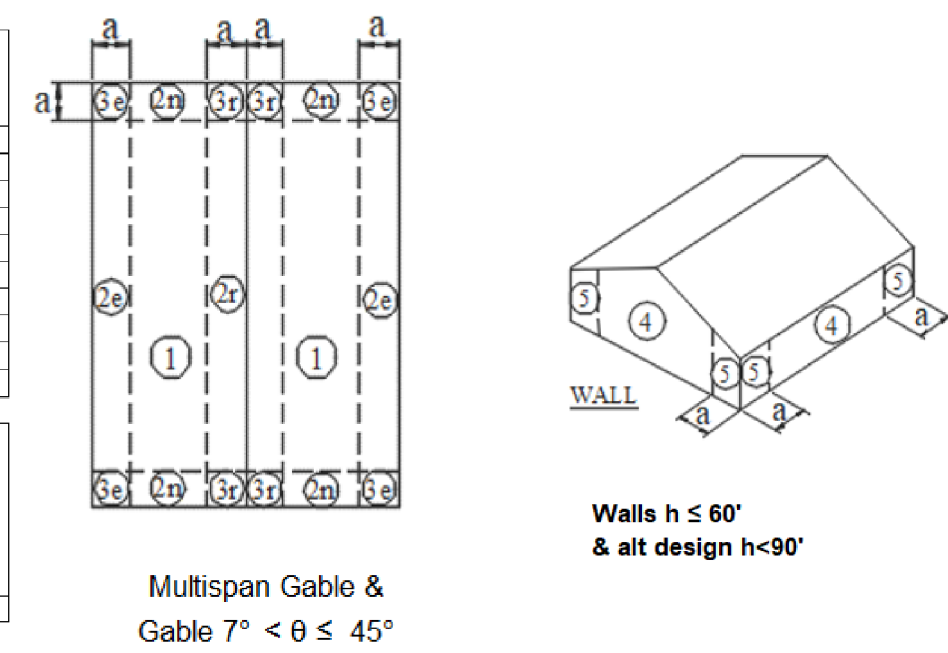


CONTRACTOR RESPONSIBILITIES

- THE WORK OF THIS PROJECT IS THE SOLE RESPONSIBILITY OF THE CONTRACTOR. SUB-CONTRACTORS AND/OR "OWNER BUILDER" WHOSE NAME APPEARS ON THE BUILDING PERMIT. (HERE AFTER REFERRED TO AS THE "CONTRACTOR") THE CONTRACTOR, SHALL CAREFULLY STUDY AND COMPARE ALL DRAWINGS, SPECIFICATIONS AND OTHER PROJECT REQUIREMENTS INCLUDING CODES AND STANDARDS IN FORCE AT THE LOCATION OF THE PROJECT. THE CONTRACTOR SHALL NOTIFY THE ENGINEER OF RECORD (EOR) IN WRITING, PRIOR TO CONSTRUCTION, OF ANY ERRORS, OMISSIONS, CODE VIOLATIONS OR CONFLICTS WHICH ARE DISCOVERED IN THE DRAWINGS, SPECIFICATIONS OR OTHER PROJECT REQUIREMENTS WITHIN 3 DAYS OF NOTICING THEM. WHERE DRAWINGS AND SPECIFICATIONS ARE CONCEPTUAL IN NATURE, THE CONTRACTOR SHALL INTERPRET THEM IN A MANNER THAT IS CONSISTENT WITH CODE REQUIREMENTS, OR ISSUE A REQUEST FOR INFORMATION (RFI) TO THE ENGINEER OF RECORD IF SOMETHING IS NOT CLEAR. SHOULD THE CONTRACTOR KNOWINGLY PROCEED WITH CONSTRUCTION BEING AWARE OF AN ISSUE OR BE UNCLEAR IN THE INTERPRETATION OF THE DRAWING THEN THE CONTRACTOR ASSUMES THAT RESPONSIBILITY. THE ENGINEER IS NOT RESPONSIBLE FOR THE COST OF THE PROJECT.
- SHOP DRAWINGS AND OTHER SUBMITTALS WILL BE REVIEWED BY THE ENGINEER AFTER THE CONTRACTOR HAS REVIEWED AND APPROVED (WITH APPROPRIATE ANNOTATIONS) SUCH SUBMITTALS. ENGINEERS REVIEW OF SUBMITTALS IS FOR DESIGN CONCEPT ONLY, AND SHALL NOT BE CONSTRUED AS A TECHNICAL REVIEW FOR THE PURPOSE OF DETERMINING COMPLETENESS OR ACCURACY OF SUBMITTALS, OR FOR DETERMINING REQUIRED QUANTITIES, DIMENSIONS OR METHODS OF INSTALLATION (ALL OF WHICH REMAIN THE RESPONSIBILITY OF THE CONTRACTOR).
- CONTRACTOR SHALL COORDINATE CLOSELY WITH OWNERS REPRESENTATIVES AND PROVIDE THEM WITH A DETAILED CONSTRUCTION SCHEDULE.
- COMPLY WITH FLORIDA ACCESSIBILITY CODE FOR BUILDING CONSTRUCTION WITH RESPECT TO DESIGN AND DIMENSIONAL STANDARDS FOR ACCESSIBLE PARKING SPACES, BUILDING ENTRY, TOILET ROOM, DIMENSIONS AND MOUNTING REQUIREMENTS FOR FIXTURES AND ACCESSORIES.
- GENERAL MATERIAL PROTECTIONS REQUIREMENTS:
 - ALL WOOD IN CONTACT WITH EARTH OR CONCRETE SHALL BE PRESSURE TREATED IN ACCORDANCE WITH A.W.P.B. STANDARDS.
 - ALL METALS SHALL BE ISOLATED FROM DISSIMILAR METAL BY INERT ISOLATION MATERIAL AS REQUIRED TO PREVENT GALVANIC CORROSION.
 - ALL METAL FOR THIS PROJECT SHALL BE HOT-DIP GALVANIZED PER ASTM G-90 OR AS SPECIFIED IN THESE DRAWINGS.
- IF APPLICABLE, THE GENERAL CONTRACTOR OR OWNER BUILDER SHALL PROVIDE ROOF COVERING FLORIDA PRODUCT OF APPROVAL SHEETS IN ADDITION TO THESE PLANS TO THE BUILDING OFFICIAL AND FOLLOW INSTALLATION INSTRUCTIONS ACCORDINGLY.
- IF APPLICABLE, THE GENERAL CONTRACTOR OR OWNER BUILDER SHALL PROVIDE WINDOW AND DOOR FLORIDA PRODUCT APPROVAL SHEETS IN ADDITION TO THESE PLANS TO THE BUILDING OFFICIAL AND FOLLOW INSTALLATION INSTRUCTIONS ACCORDINGLY.
- CONTRACTOR SHALL FIELD VERIFY ALL DIMENSIONS AND EXISTING CONDITIONS. CONTRACTOR SHALL INFORM E.O.R. OF ANY VARIATIONS FROM THIS PLAN SET.

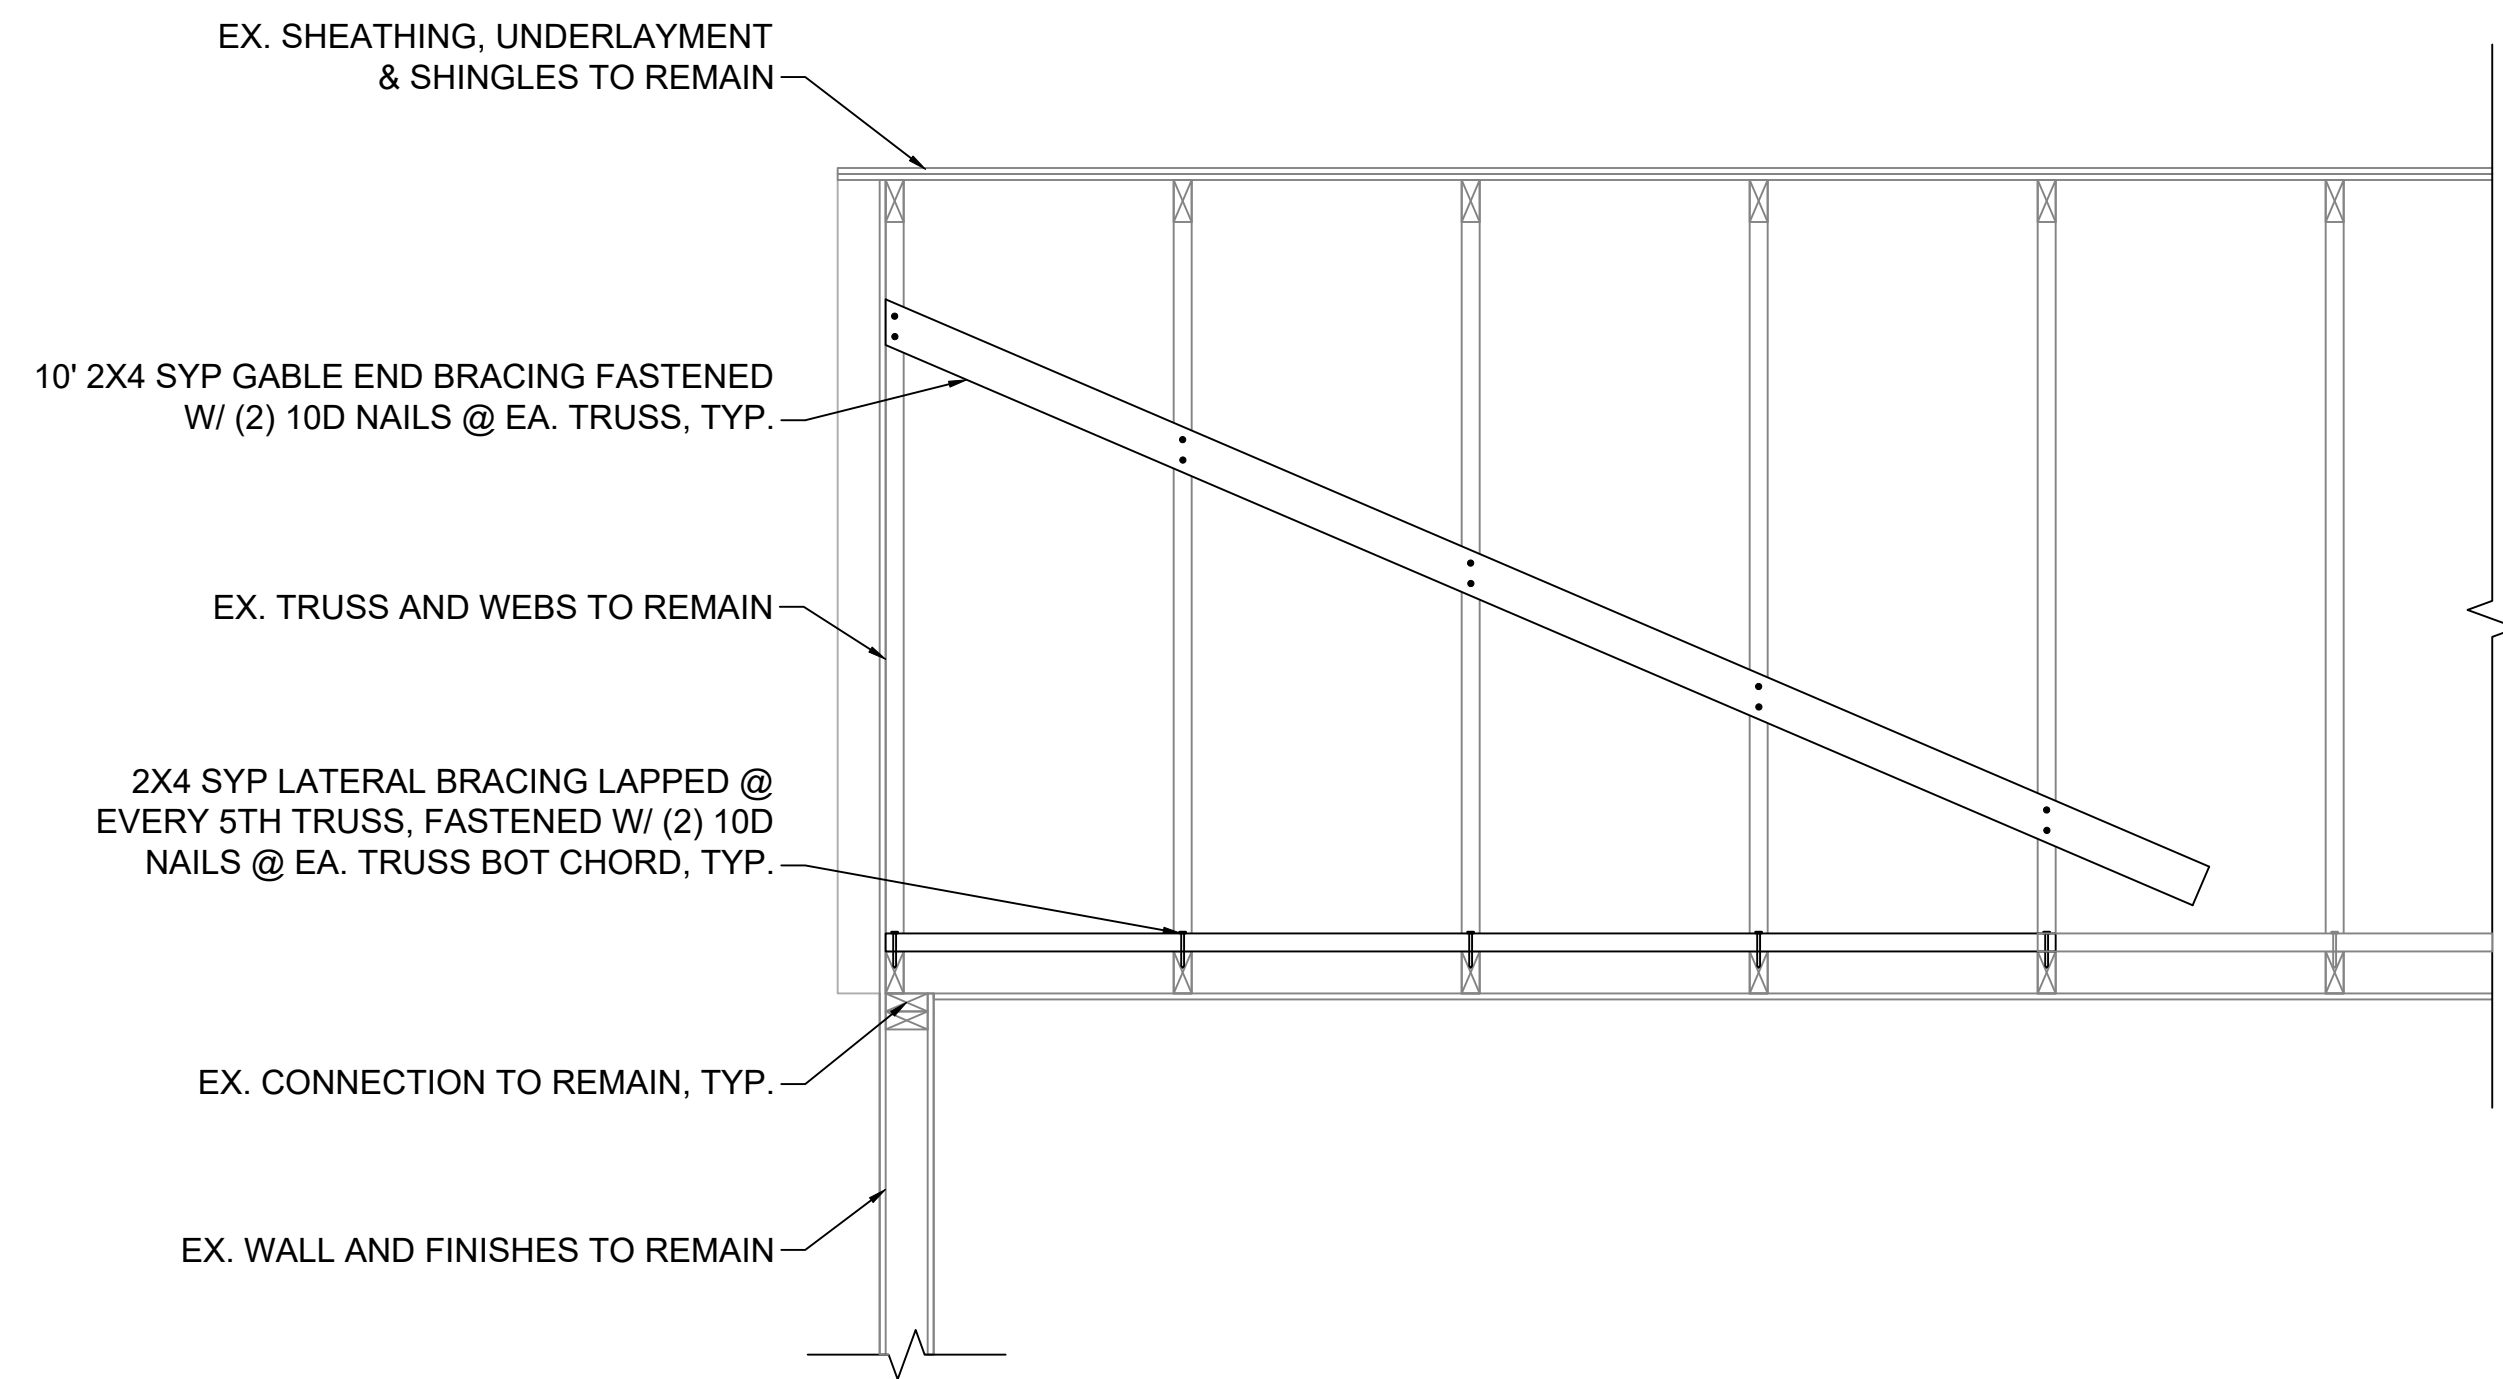

CROSS SECTION
SCALE 3/4" = 1'

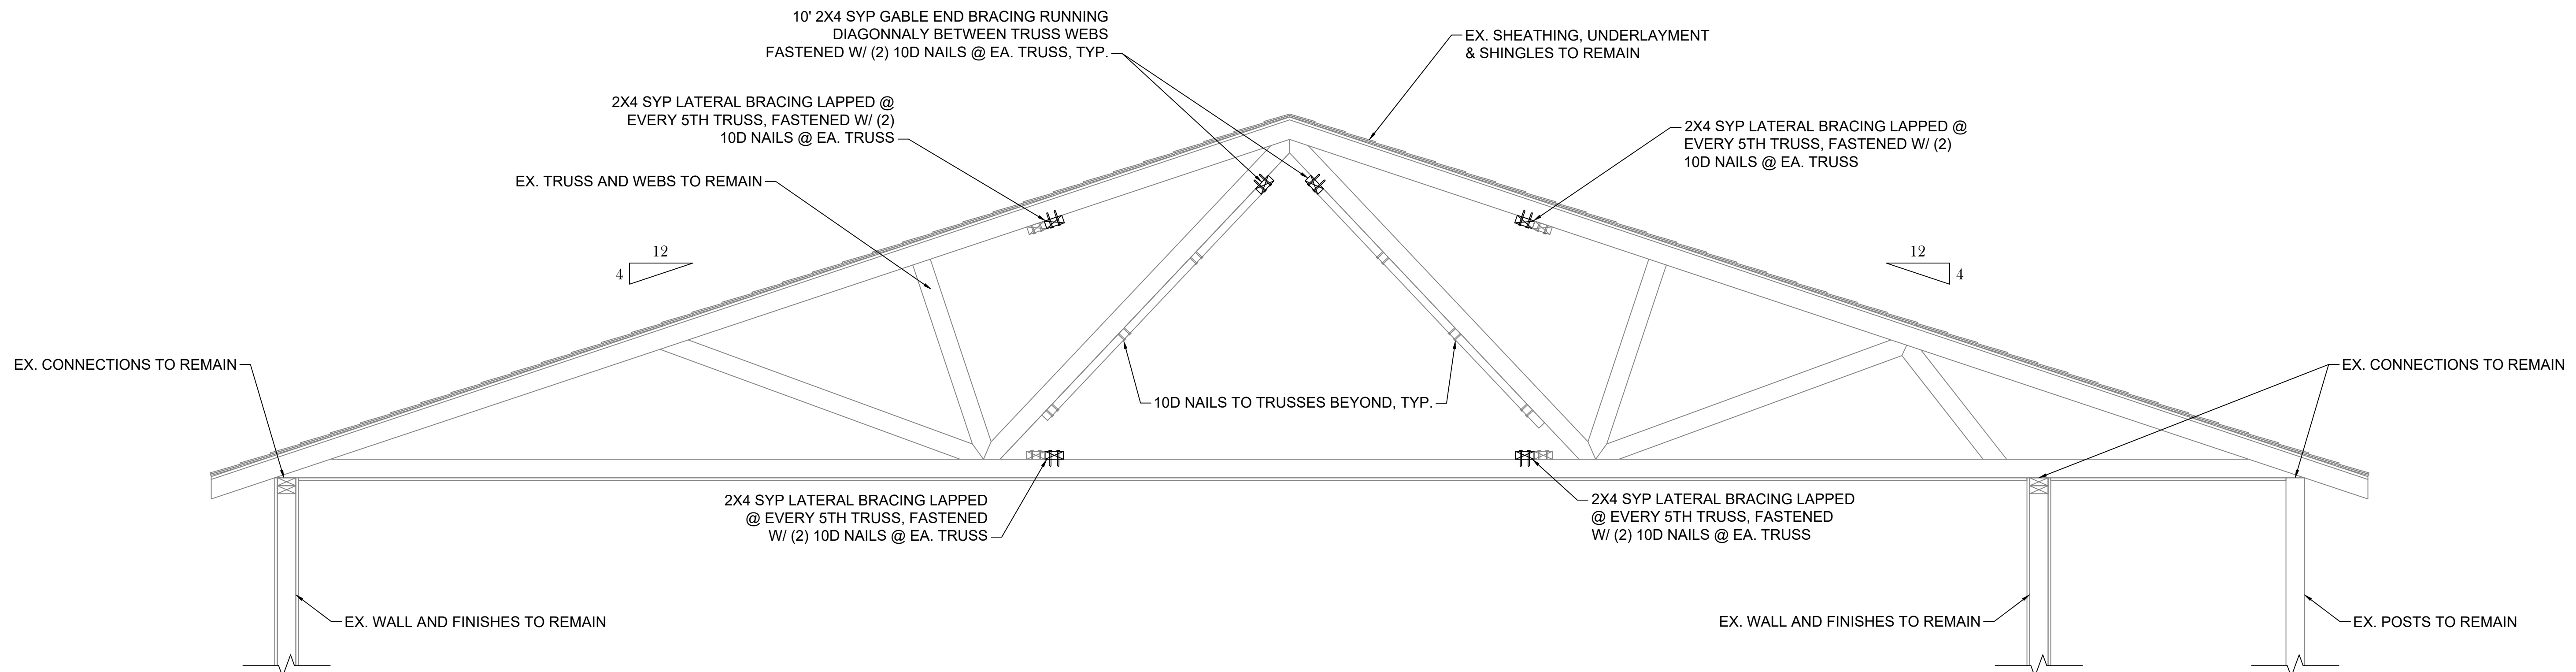

B **CROSS SECTION**
S-2 S-1 SCALE 3/4" = 1'

PROJECT BISHOP RD
TRUSS REINF.

FOR REVIEW

ADVANCED ENGINEERING PROJECT NUMBER
26056

This drawing is the property of Advanced
Engineering and is not to be reproduced or copied
in whole or in part.



ENGINEER OF RECORD: PETER D. MILLER, P.E.
FLORIDA P.E. LICENSE NO.: 104758
FLORIDA REGISTRY NO: 28038
NOT APPROVED FOR PERMIT UNLESS
DULY SIGNED AND SEALED BY ENGINEER

PETER D. MILLER, STATE OF FLORIDA,
PROFESSIONAL ENGINEER, LICENSE NO. 104758
THIS ITEM HAS BEEN DIGITALLY SIGNED AND SEALED BY
PETER D. MILLER ON THE DATE INDICATED HERE.
SIGNATURE MUST BE VERIFIED ON ANY ELECTRONIC COPIES.

PER RULE 61G15-23.004 (3)(D)(2) WHEN A DIGITALLY CREATED
SEAL IS NOT USED AND PARAGRAPH (E) "A DIGITAL SIGNATURE
APPLIED TO AN ITEM IN ELECTRONIC FORM SHALL HAVE THE
SAME FORCE AND EFFECT AS SIGNING ALL OF THE INDIVIDUAL
SHEETS OR PAGES CONTAINED WITHIN THAT ITEM UNLESS
OTHERWISE LIMITED AS SPECIFIED IN SUBSECTION
61G15-30.003(3), F.A.C."

THESE PLANS WERE PREPARED IN ACCORDANCE TO F.S. CHAPTER 471 AND APPLICABLE FLORIDA BUILDING CODE 8TH EDITION, 2023. ANY SERVICES OF AN ARCHITECTURAL NATURE REFLECTED IN THIS PLAN ARE BEING PROVIDED BY ADVANCED ENGINEERING CONSULTANTS LLC PURSUANT TO SECTION 471.003(3), F.S. THIS DESIGN IS SITE SPECIFIC AND MAY NOT BE USED AT OTHER LOCATIONS WITHOUT THE CONSENT OF ADVANCED ENGINEERING CONSULTANTS LLC. ANY REVISIONS TO THESE PLANS MUST BE IN ACCORDANCE WITH THE SPECIFICATIONS AND COMPUTER FILES, PREPARED BY ADVANCED ENGINEERING CONSULTANTS LLC. SHALL REMAIN THE PROPERTY OF ADVANCED ENGINEERING CONSULTANTS LLC. ANY REUSE OF THESE PLANS, IN PART OR WHOLE, WITHOUT THE EXPRESSED, WRITTEN, CONSENT OF ADVANCED ENGINEERING CONSULTANTS LLC, ADVANCED ENGINEERING CONSULTANTS LLC, WILL VIOLATE ALL COMMON LAW, STATUTORY AND OTHER RESERVATION RIGHTS, INCLUDING THE COPYRIGHT THERE TO.

DRAWINGS

STRUCTURAL SET

REVISIONS		
No.	Date	Description

PLANS TO BE PRINTED IN COLOR

DRAWN & DESIGNED BY

CB

CHECKED BY
PM, MH

INITIAL RELEASE DATE
2026-07-22

SHEET TITLE

STRUCTURAL DETAILS

PLANS ARE TO BE PRINTED IN COLOR

SCALE

AS NOTED

SHEET NUMBER

S-2

PLANS TO BE PRINTED IN COLOR