


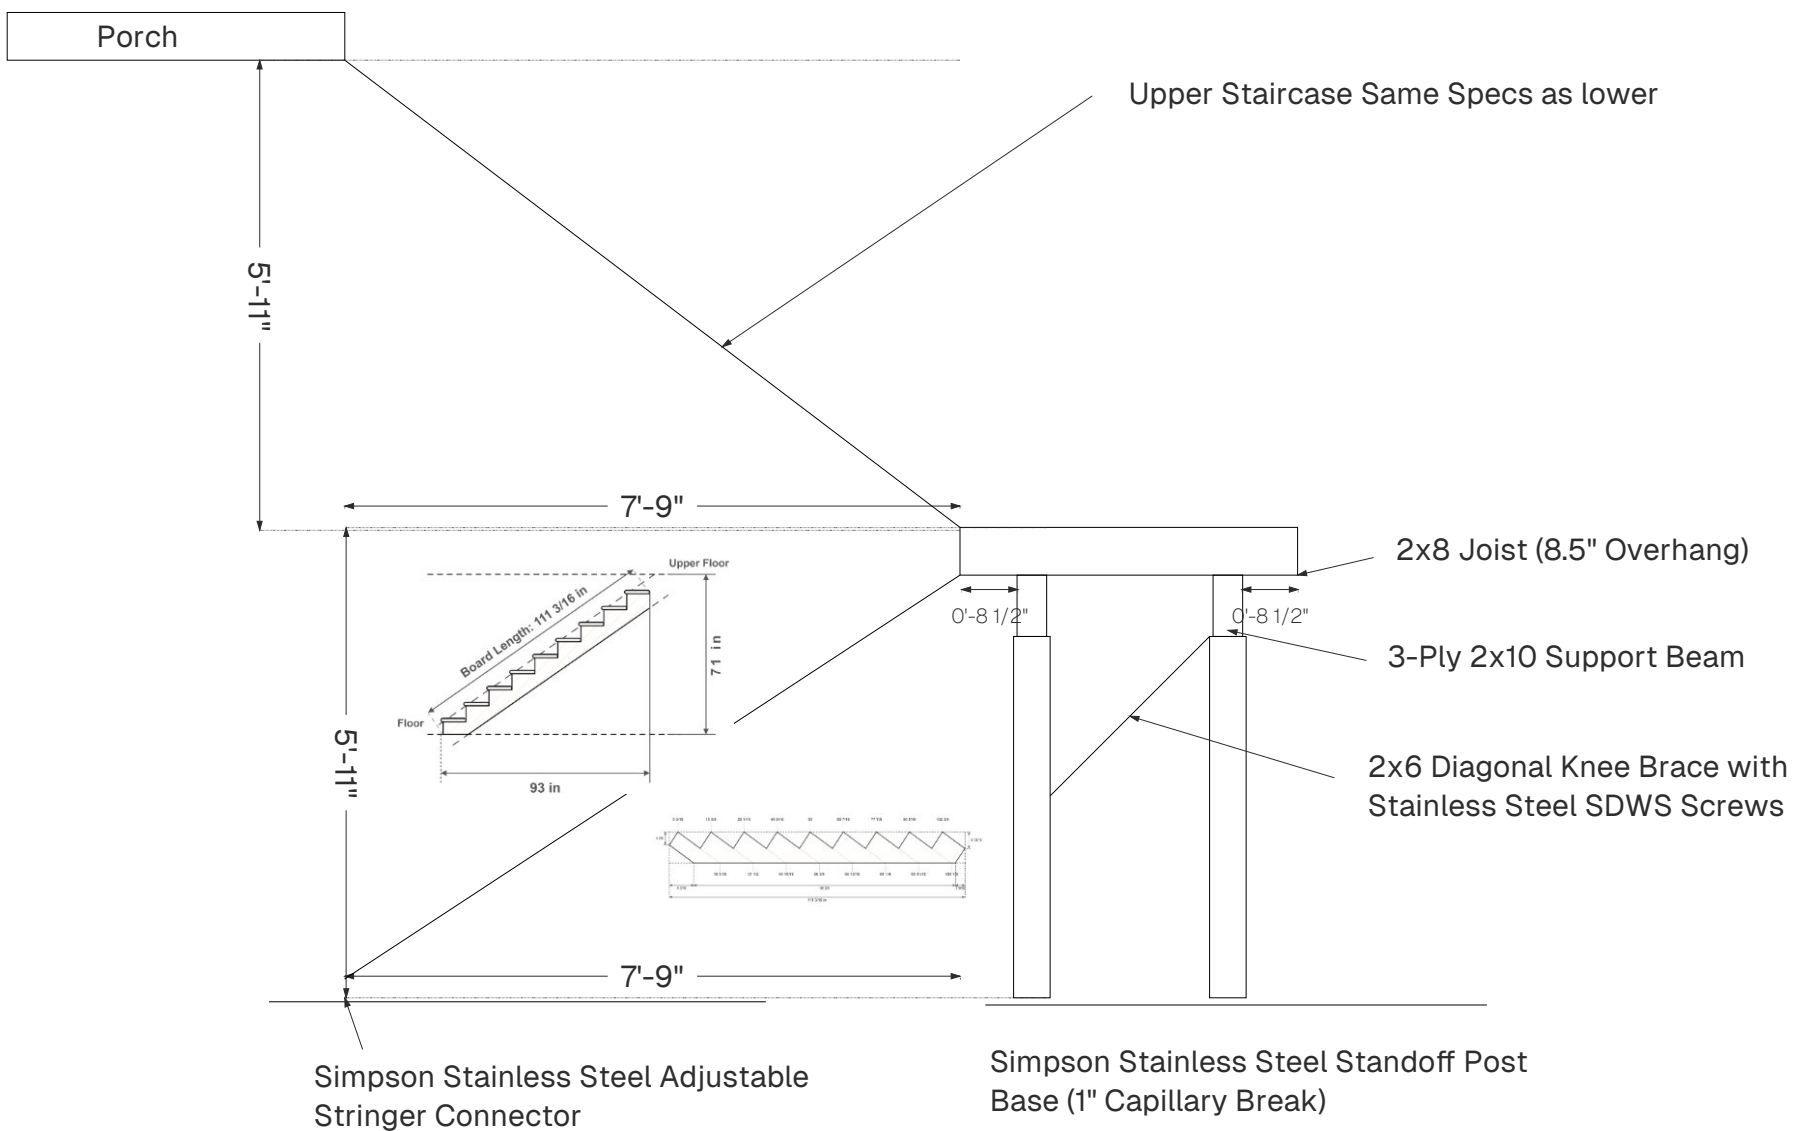

Stair Geometry: Stair rise and run strictly comply with FRC Section R311.7. Maximum riser height is 7¾ inches and minimum tread depth is 10 inches. Clear stair width is a minimum of 36 inches with 3x independent UC4B stringers.

Wind Uplift & Lateral Load Path: Solid post-to-beam connection achieved via Simpson stainless steel post caps. Diagonal knee bracing installed at 45 degrees to prevent racking from high coastal winds.

Concrete Anchor Layout: All stainless steel concrete fasteners are drilled vertically down into the slab. New anchor locations maintain a minimum 4-inch clearance from all exposed vertical concrete edges and a minimum 4-to-6-inch clearance from remediated 2003 anchor points.