

DRAWINGS INDEX:

SHEET NUMBER	SHEET NAME
Sheet 001	COVER PAGE
Sheet 002	FLOOR PLAN
Sheet 003	PROPOSED FLOOR PLAN
Sheet 004	SITE PLAN
Sheet 005	ISOMETRIC VIEW
Sheet 006	DETAILS
Sheet 007	NOTES
Sheet 008	
Sheet 009	
Sheet 010	
Sheet 011	

GENERAL NOTES GARAGE ENCLOSURE:

1. ALL STRUCT. LUMBER, WHERE REQ'D, SHALL BE #2 SYP OR APPROVED EQ.
2. ALL WORK SHALL COMPLY W/ FBC 8TH ED. (2023) & APPLICABLE MARION CO. REQ'S.
3. PROVIDE NEW 36" x 80" EXT. GARAGE SIDE DOOR OPENING AS SHOWN.
4. SAW-CUT & REMOVE EXIST. WALL ONLY AS REQ'D FOR NEW OPENING. PROTECT ADJ. CONST.
5. PROVIDE REQ'D LINTEL/HEADER, REINF., GROUTED CELLS & JAMB SUPPORT PER STRUCT. DETAILS.
6. DOWELS/ANCHORS INTO EXIST. CONC./CMU SHALL USE APPROVED STRUCT. EPOXY PER MFR. REQ'S.
7. DO NOT CUT OR MODIFY EXIST. STRUCT. MEMBERS EXCEPT AS SHOWN.
8. NEW EXT. DOOR & FRAME SHALL COMPLY W/ APPLICABLE FL PRODUCT APPROVAL & WIND-LOAD REQ'S.
9. INSTALL DOOR PLUMB, LEVEL & ANCHORED PER APPROVED MFR. INSTALLATION INSTRUCTIONS.
10. FLASH, CAULK & SEAL ALL EXT. JOINTS TO PREVENT WATER INTRUSION.
11. PATCH & FINISH DISTURBED INT./EXT. SURFACES TO MATCH EXIST.
12. FIELD VERIFY ALL DIM., WALL CONDITIONS & UTILITIES PRIOR TO CUTTING.
13. REPORT FIELD DISCREPANCIES TO ENGINEER PRIOR TO PROCEEDING.
14. ALL STRUCT. REINF., LINTELS & ANCHORAGE SHALL BE INSPECTED, WHERE REQ'D, PRIOR TO CONCEALMENT.

STRUCTURAL NOTES — GARAGE 36IN. X 80IN. EXTERIOR SIDE DOOR GARAGE:

- 1.- THE STRUCTURAL INTEGRITY OF THE WORK DEPICTED IN THESE DRAWINGS IS CONTINGENT UPON COMPLETION IN ACCORDANCE WITH THE APPROVED PLANS, SPECIFICATIONS, AND STRUCTURAL DETAILS. CONTRACTOR SHALL PROVIDE ALL TEMPORARY SHORING AND BRACING REQUIRED TO MAINTAIN THE STABILITY OF THE EXISTING WALL AND ADJACENT CONSTRUCTION DURING CREATION OF THE NEW DOOR OPENING AND UNTIL ALL PERMANENT STRUCTURAL CONNECTIONS ARE COMPLETED.
- 2.- THE ENGINEER ASSUMES NO RESPONSIBILITY FOR CONSTRUCTION MEANS, METHODS, SEQUENCES, PROCEDURES, TEMPORARY BRACING, OR JOBSITE SAFETY UNLESS SUCH ITEMS ARE SPECIFICALLY DESIGNED AND DETAILED BY THE ENGINEER.
- 3.- THESE DRAWINGS ADDRESS THE STRUCTURAL WORK ASSOCIATED WITH CREATING A NEW OPENING IN THE EXISTING EXTERIOR GARAGE WALL FOR INSTALLATION OF ONE NEW 36-INCH x 80-INCH EXTERIOR SIDE DOOR. ELECTRICAL, MECHANICAL, PLUMBING, SURVEY, AND OTHER WORK NOT SPECIFICALLY SHOWN SHALL BE COORDINATED BY THE CONTRACTOR AND SHALL COMPLY WITH ALL APPLICABLE CODES.
- 4.- CONTRACTOR SHALL FIELD VERIFY ALL EXISTING DIMENSIONS, ELEVATIONS, SLAB AND FOUNDATION CONDITIONS, WALL THICKNESS, WALL CONSTRUCTION, EXISTING REINFORCEMENT WHERE IDENTIFIABLE, AND LOCATION OF THE PROPOSED DOOR OPENING PRIOR TO COMMENCING WORK. ANY DISCREPANCY AFFECTING THE STRUCTURAL WORK SHALL BE REPORTED TO THE ENGINEER PRIOR TO CONSTRUCTION.
- 5.- THE NEW DOOR OPENING SHALL BE ACCURATELY LAID OUT AND CUT INTO THE EXISTING WALL AT THE LOCATION AND DIMENSIONS INDICATED ON THE APPROVED DRAWINGS. CUTTING AND DEMOLITION SHALL BE PERFORMED IN A CONTROLLED MANNER TO MINIMIZE DAMAGE TO ADJACENT CONSTRUCTION.
- 6.- EXISTING STRUCTURAL ELEMENTS OUTSIDE THE LIMITS OF THE NEW DOOR OPENING SHALL NOT BE CUT, DAMAGED, REMOVED, OR MODIFIED UNLESS SPECIFICALLY INDICATED ON THE APPROVED STRUCTURAL DRAWINGS.
- 7.- PROVIDE THE REQUIRED STRUCTURAL LINTEL, HEADER, BOND BEAM, REINFORCEMENT, GROUT-FILLED CELLS, REINFORCED JAMBS, OR OTHER STRUCTURAL SUPPORT AT THE NEW DOOR OPENING AS INDICATED ON THE APPROVED STRUCTURAL DETAILS.
- 8.- WHERE NEW REINFORCING STEEL, DOWELS, ANCHORS, OR OTHER STRUCTURAL CONNECTIONS ARE REQUIRED TO CONNECT TO EXISTING CONCRETE OR MASONRY, INSTALL USING THE SPECIFIED APPROVED STRUCTURAL ANCHORING SYSTEM. EMBEDMENT DEPTH, HOLE DIAMETER, SPACING, EDGE DISTANCE, HOLE CLEANING, AND INSTALLATION SHALL COMPLY WITH THE STRUCTURAL DETAILS AND MANUFACTURER'S APPROVED INSTALLATION REQUIREMENTS.
- 9.- THE NEW 36-INCH x 80-INCH EXTERIOR DOOR ASSEMBLY SHALL BE INSTALLED PLUMB, LEVEL, SQUARE, AND SECURELY ANCHORED TO THE STRUCTURALLY SUPPORTED OPENING IN ACCORDANCE WITH THE APPROVED PRODUCT INSTALLATION INSTRUCTIONS AND STRUCTURAL DETAILS.
- 10.- THE EXTERIOR DOOR ASSEMBLY, FRAME, FASTENERS, ANCHORS, AND ASSOCIATED COMPONENTS SHALL COMPLY WITH APPLICABLE FLORIDA PRODUCT APPROVAL AND DESIGN WIND-PRESSURE REQUIREMENTS FOR THE PROJECT LOCATION. PRODUCT APPROVAL AND INSTALLATION REQUIREMENTS SHALL BE VERIFIED PRIOR TO INSTALLATION.
- 11.- ALL EXTERIOR PERIMETERS OF THE NEW DOOR FRAME SHALL BE PROPERLY FLASHED, SEALED, AND WEATHERPROOFED TO PREVENT WATER INTRUSION. DISTURBED EXTERIOR FINISHES SHALL BE RESTORED TO PROVIDE A COMPLETE WEATHER-RESISTANT ASSEMBLY COMPATIBLE WITH THE EXISTING CONSTRUCTION.
- 12.- INTERIOR WALL SURFACES DISTURBED BY THE NEW DOOR OPENING SHALL BE PATCHED AND REPAIRED AS REQUIRED. NEW INTERIOR FINISHES SHALL BE COMPLETED, TEXTURED, AND PREPARED TO MATCH THE ADJACENT EXISTING CONSTRUCTION AS CLOSELY AS PRACTICABLE.
- 13.- NEW CONSTRUCTION SHALL NOT OBSTRUCT OR INTERFERE WITH EXISTING ELECTRICAL, PLUMBING, MECHANICAL, ROOF, ATTIC, OR OTHER BUILDING SYSTEMS. EXISTING UTILITIES SHALL BE IDENTIFIED PRIOR TO CUTTING THE WALL. ANY CONFLICT SHALL BE REPORTED BEFORE PROCEEDING WITH THE AFFECTED WORK.
- 14.- ALL MANUFACTURED PRODUCTS, DOOR COMPONENTS, ANCHORS, FASTENERS, STRUCTURAL ADHESIVES, LINTELS, AND OTHER COMPONENTS SHALL BE INSTALLED IN ACCORDANCE WITH THEIR APPROVED MANUFACTURER'S INSTALLATION INSTRUCTIONS AND APPLICABLE PRODUCT APPROVALS. NOTHING IN THESE DRAWINGS SHALL BE INTERPRETED TO OVERRIDE AN APPROVED PRODUCT INSTALLATION REQUIREMENT.
- 15.- CONTRACTOR IS RESPONSIBLE FOR VERIFYING ALL EXISTING CONDITIONS, DIMENSIONS, AND DETAILS PRIOR TO CONSTRUCTION. DO NOT SCALE DRAWINGS. WRITTEN DIMENSIONS AND APPROVED STRUCTURAL DETAILS SHALL GOVERN.
- 16.- ALL WORK SHALL COMPLY WITH THE FLORIDA BUILDING CODE, 8TH EDITION (2023), APPLICABLE REFERENCED STANDARDS, AND MARION COUNTY REQUIREMENTS. REQUIRED INSPECTIONS SHALL BE COMPLETED PRIOR TO CONCEALING STRUCTURAL REINFORCEMENT, ANCHORAGE, LINTELS, GROUTED CELLS, OR OTHER WORK REQUIRING INSPECTION.


MARION COUNTY

3990 SW 34TH TERRACE RD, OCALA, FL 34473


GARCIA CASTILLO ISDEL AMADOR

GARAGE EXTERIOR WALL ALTERATION – NEW 36" x 80" SIDE DOOR

ARIAL VIEW

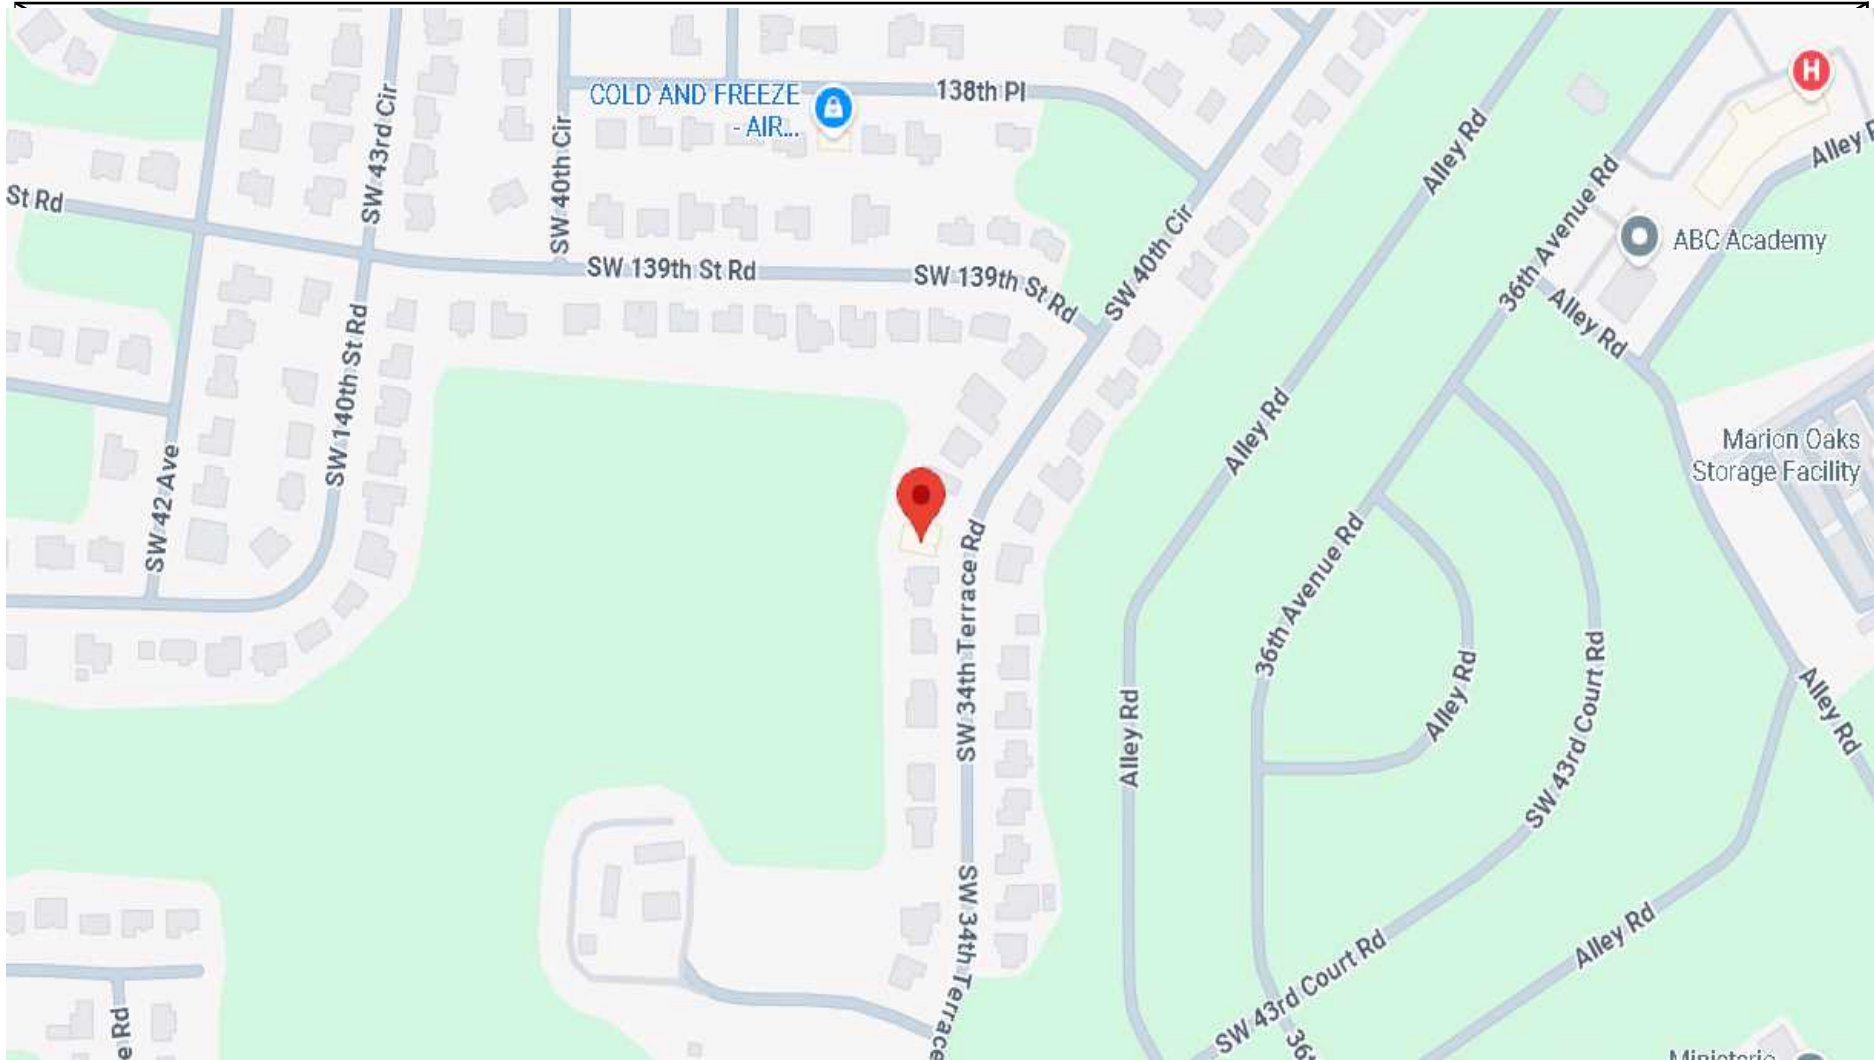

SATELITE VIEW

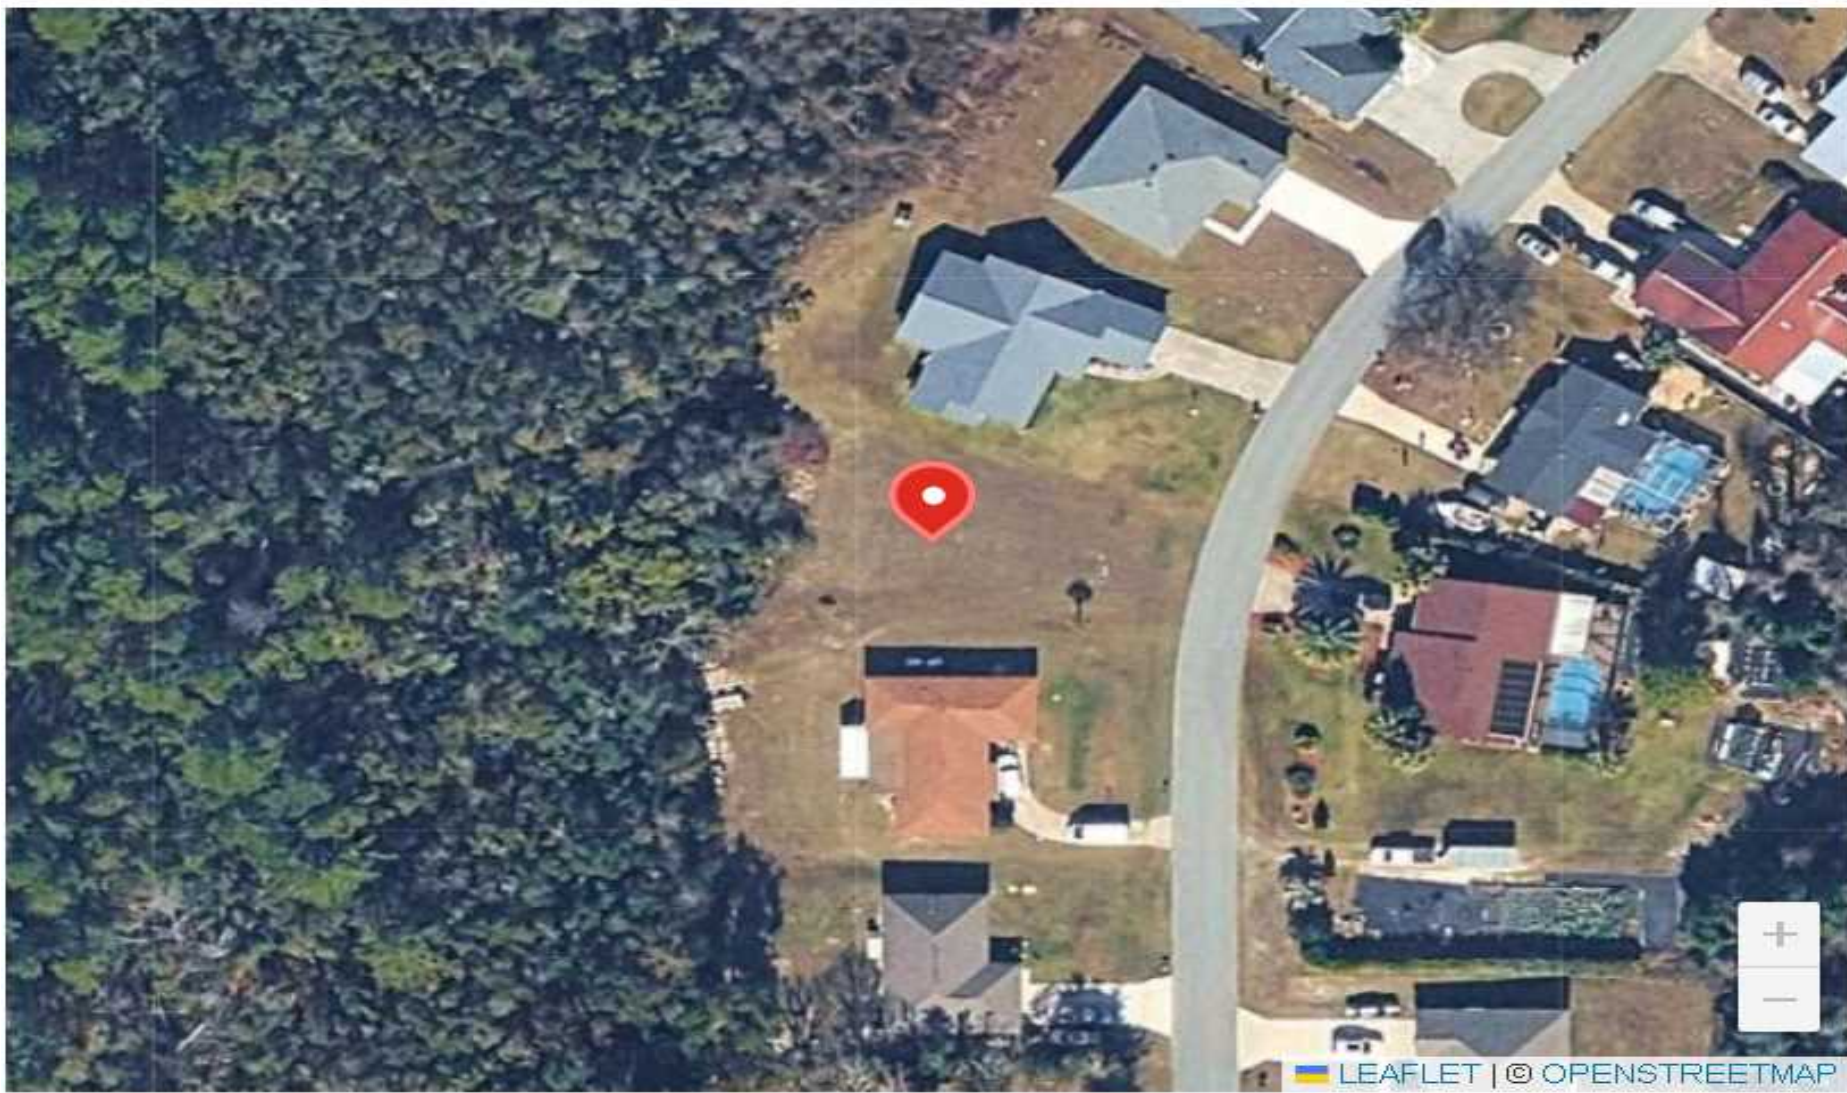

FRONT VIEW



SITE INFORMATION:

CUSTOMER NAME:

GARCIA CASTILLO ISDEL AMADOR

PROJECT ADDRESS:

13990 SW 34TH TERRACE RD, OCALA, FL 34473

CUSTOMER CELLPHONE #:

(201) 952-2829

CUSTOMER EMAIL:

ISDELGARCIA1997@GMAIL.COM


CONTRACTOR INFORMATION:

SEATING CONTRACTORS USA.
19815 STATE ROAD 52
LAND O LAKES Florida 34637
813-505-7560
C/C 1505749
(813) 505-7650
Phll@seatingusa.com

OTHER DETAILS:

PROPERTY SEA LEVEL ELEVATION: 60 FT.
PROPERTY GEO LOCATION CODENATES:
29.01867924348934, -82.1879086045466
ATC HAZARD ASCE 7-22
RISK CATEGORY: II

FLORIDA ULTIMATE DESIGN WIND SPEED

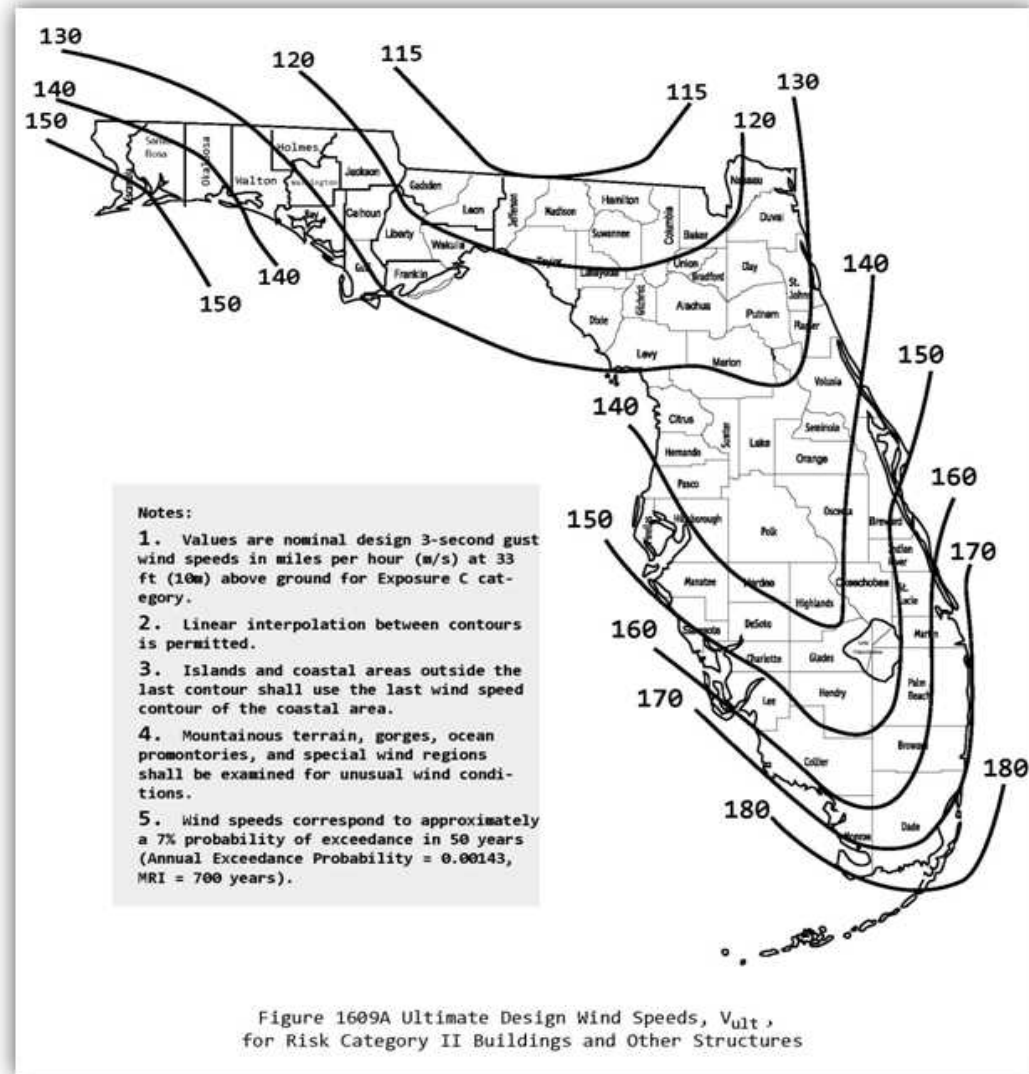

PROJECT OVERVIEW:

THIS RENOVATION PROJECT CONSISTS OF THE MODIFICATION OF AN EXISTING EXTERIOR GARAGE WALL TO CREATE A NEW DOOR OPENING FOR THE INSTALLATION OF ONE NEW 36-INCH x 80-INCH EXTERIOR SIDE DOOR.

THE SCOPE OF WORK INCLUDES LAYOUT AND CONTROLLED CUTTING AND REMOVAL OF THE EXISTING CONCRETE MASONRY WALL AS REQUIRED TO FORM THE NEW DOOR OPENING. ALL CUTTING AND DEMOLITION SHALL BE PERFORMED IN A CONTROLLED MANNER TO PREVENT DAMAGE TO ADJACENT EXISTING CONSTRUCTION AND TO MAINTAIN THE STRUCTURAL INTEGRITY OF THE REMAINING WALL ASSEMBLY.

THE NEW DOOR OPENING SHALL RECEIVE THE REQUIRED STRUCTURAL SUPPORT, INCLUDING AN APPROVED LINTEL OR HEADER AS APPLICABLE, REINFORCEMENT, GROUT-FILLED CELLS, ANCHORAGE, AND OTHER STRUCTURAL COMPONENTS AS INDICATED ON THE APPROVED CONSTRUCTION DOCUMENTS AND STRUCTURAL DETAILS.

ONE NEW 36-INCH x 80-INCH EXTERIOR DOOR ASSEMBLY SHALL BE INSTALLED WITH APPROVED FASTENERS AND ANCHORAGE, FLASHING, SEALANTS, AND WEATHERPROOFING. THE DOOR ASSEMBLY SHALL COMPLY WITH APPLICABLE FLORIDA PRODUCT APPROVAL AND WIND-LOAD REQUIREMENTS FOR THE PROJECT LOCATION.

ALL DISTURBED INTERIOR AND EXTERIOR WALL SURFACES AROUND THE NEW OPENING SHALL BE PROPERLY REPAIRED AND FINISHED TO PROVIDE A COMPLETE WEATHER-RESISTANT ASSEMBLY AND TO MATCH THE ADJACENT EXISTING CONSTRUCTION AS CLOSELY AS PRACTICABLE.

ALL EXISTING CONDITIONS, WALL CONSTRUCTION, OPENING DIMENSIONS, AND FIELD DIMENSIONS SHALL BE VERIFIED PRIOR TO CONSTRUCTION. NO STRUCTURAL MEMBER SHALL BE CUT, REMOVED, OR MODIFIED EXCEPT AS SPECIFICALLY INDICATED ON THE APPROVED CONSTRUCTION DOCUMENTS AND STRUCTURAL DETAILS.

ALL WORK SHALL BE COMPLETED IN ACCORDANCE WITH THE FLORIDA BUILDING CODE, 8TH EDITION (2023), APPLICABLE FLORIDA PRODUCT APPROVAL REQUIREMENTS, MANUFACTURER INSTALLATION INSTRUCTIONS, APPROVED STRUCTURAL DETAILS, AND ALL APPLICABLE LOCAL AND STATE REQUIREMENTS.

APPLICABLE GOVERNING CODES& NOTES:


SYSTEM SHALL BE INSTALLED UNDER THE FOLLOWING CODES AND STANDARDS:

- 1) 2023 FLORIDA BUILDING CODE – BUILDING, 8TH EDITION.
- 2) 2023 FLORIDA BUILDING CODE – RESIDENTIAL, 8TH EDITION.
- 3) 2020 NATIONAL ELECTRICAL CODE (NEC / NFPA 70).
- 4) 2023 FLORIDA FIRE PREVENTION CODE (FFPC), 8TH EDITION.
- 5) APPLICABLE MARION COUNTY ORDINANCES, LOCAL AMENDMENTS, AND REQUIREMENTS.

SITE SPECIFICATIONS:

CONSTRUCTION: SINGLE FAMILY DWELLING (SFD)
ZONING: R-1 RESIDENTIAL
NO. OF STORY: TWO STORY EXPOSURE CATEGORY: B, RISK CATEGORY: II
WIND SPEED (ASCE 7-22): **140 MPH**
GROUND SNOW LOAD (ASCE 7-22): 0 lb/sqft
ASHRAE EXTREME LOW: 1°C
ASHRAE HIGH TEMP (**2% AVG**): **34°C**
ASHRAE DISTANCE ABOVE ROOF (7/8"): 56"
PARCEL ID: **8001-0201-39**

This drawings are sole property of Seating Constructors USA, Unless otherwise provided for by contract, or the writing means, the contents of this drawing are confidential & shall be not transmitted to any other party accepted and agreed by Smart Choice Contractors USA. 2025 Copyright.

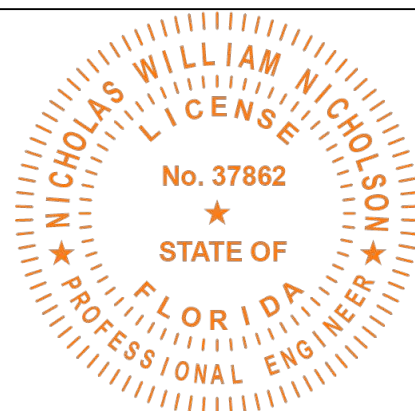SHEET TITLE COVER PAGE	CUSTOMER NAME: GARCIA CASTILLO ISDEL AMADOR	CUSTOMER INFORMATION Email: ISDELGARCIA1997@GMA Phone: IL.COM(201) 952-2829		NICHOLSON ENGINEERING ASSOCIATES, INC. 7468 Horse Lake Rd, Brooksville, FL 34601 Phone: 352.799.0170 Fax: 352.754.9167		REVISIONS				01
	MM/DD/Y					DRAWINGS REMARKS				
	1	01.07.26				GARAGE EXTERIOR WALL ALTERATION – NEW 36" x 80" SIDE DOOR				
	2									
						3				
						PROJECT NUMBER: 0024598		DESIGN DATE: 01.07.26		