

INDEX OF DRAWINGS:	
SHEET #	SHEET NAME
Sheet 001	COVER PAGE
A-01	FLOOR PLAN
A-02	LIFE SAFETY PLAN
A-03	CUT SHEETS
A-04	ISO DETAILS

EXISTING CONDITIONS NOTES:

GENERAL:

THE PURPOSE OF THESE DRAWINGS IS TO DOCUMENT EXISTING CONDITIONS OF THE RESTAURANT FACILITY FOR REVIEW BY THE FLORIDA DEPARTMENT OF BUSINESS AND PROFESSIONAL REGULATION (DBPR).

NO STRUCTURAL, ARCHITECTURAL, MECHANICAL, ELECTRICAL, PLUMBING, FIRE PROTECTION, OR LIFE SAFETY MODIFICATIONS ARE INCLUDED IN THIS SUBMITTAL.

ALL BUILDING COMPONENTS, STRUCTURAL ELEMENTS, WALLS, FLOORS, CEILINGS, ROOF SYSTEMS, OPENINGS, FINISHES, FIXTURES, EQUIPMENT, AND UTILITIES SHOWN ON THESE DRAWINGS ARE EXISTING UNLESS OTHERWISE NOTED.

THE DRAWINGS ARE INTENDED SOLELY AS A RECORD OF EXISTING CONDITIONS AND SHALL NOT BE CONSTRUED AS CONSTRUCTION DOCUMENTS.

NO CHANGE OF OCCUPANCY IS PROPOSED UNDER THIS SUBMITTAL.

NO INCREASE IN OCCUPANT LOAD IS PROPOSED UNDER THIS SUBMITTAL.

NO ALTERATIONS TO MEANS OF EGRESS, EXIT ACCESS, EXIT DISCHARGE, OR LIFE SAFETY SYSTEMS ARE PROPOSED UNDER THIS SUBMITTAL.

NO ALTERATIONS TO THE EXISTING FIRE-RATED ASSEMBLIES, FIRE BARRIERS, FIRE ALARM SYSTEMS, OR FIRE SUPPRESSION SYSTEMS ARE INCLUDED IN THIS SUBMITTAL.

NO MODIFICATIONS TO EXISTING ELECTRICAL SERVICE, PANELBOARDS, BRANCH CIRCUITS, LIGHTING SYSTEMS, OR EMERGENCY SYSTEMS ARE INCLUDED IN THIS SUBMITTAL.

NO MODIFICATIONS TO EXISTING PLUMBING SYSTEMS, SANITARY SYSTEMS, WATER DISTRIBUTION SYSTEMS, GREASE INTERCEPTORS, OR GAS PIPING SYSTEMS ARE INCLUDED IN THIS SUBMITTAL.

NO MODIFICATIONS TO EXISTING MECHANICAL, VENTILATION, AIR CONDITIONING, OR EXHAUST SYSTEMS ARE INCLUDED IN THIS SUBMITTAL.

ALL EXISTING CONDITIONS SHOWN ARE BELIEVED TO BE SUBSTANTIALLY IN ACCORDANCE WITH THE APPLICABLE FLORIDA BUILDING CODE, FLORIDA FIRE PREVENTION CODE, FLORIDA ACCESSIBILITY CODE, FLORIDA PLUMBING CODE, FLORIDA MECHANICAL CODE, FLORIDA BUILDING CODE ELECTRICAL, AND APPLICABLE DBPR REQUIREMENTS IN EFFECT AT THE TIME OF THIS SUBMITTAL.

ANY EXISTING CONDITIONS FOUND DURING FUTURE INSPECTIONS OR RENOVATIONS THAT DO NOT COMPLY WITH CURRENT APPLICABLE CODES SHALL BE CORRECTED UNDER A SEPARATE PERMIT AS REQUIRED BY THE AUTHORITY HAVING JURISDICTION.

STRUCTURAL

ALL STRUCTURAL COMPONENTS SHOWN ON THESE DRAWINGS ARE EXISTING.

NO STRUCTURAL ALTERATIONS, ADDITIONS, REMOVALS, OR REPAIRS ARE INCLUDED IN THIS SUBMITTAL.

NO MODIFICATIONS TO EXISTING FOUNDATIONS, FOOTINGS, CONCRETE SLABS, LOAD-BEARING WALLS, BEAMS, COLUMNS, ROOF FRAMING, FLOOR FRAMING, OR LATERAL FORCE RESISTING SYSTEMS ARE INCLUDED IN THIS SUBMITTAL.

THE EXISTING BUILDING STRUCTURE IS TO REMAIN UNCHANGED.

MECHANICAL

ALL MECHANICAL EQUIPMENT, DUCTWORK, AIR DISTRIBUTION DEVICES, EXHAUST SYSTEMS, AND VENTILATION COMPONENTS SHOWN ARE EXISTING TO REMAIN.

ELECTRICAL

ALL ELECTRICAL EQUIPMENT, PANELS, LIGHTING FIXTURES, RECEPTACLES, SWITCHES, AND ASSOCIATED WIRING SHOWN ARE EXISTING TO REMAIN.

PLUMBING

ALL PLUMBING FIXTURES, SANITARY PIPING, WATER DISTRIBUTION PIPING, GREASE MANAGEMENT EQUIPMENT, AND RELATED COMPONENTS SHOWN ARE EXISTING TO REMAIN.

FIRE AND LIFE SAFETY

EXISTING FIRE EXTINGUISHERS, EXIT SIGNS, EMERGENCY LIGHTING, FIRE ALARM COMPONENTS, AND FIRE SUPPRESSION SYSTEMS, WHERE PRESENT, ARE EXISTING TO REMAIN.

ACCESSIBILITY

NO MODIFICATIONS TO ACCESSIBLE ROUTES, ACCESSIBLE SEATING, ACCESSIBLE TOILET FACILITIES, OR ACCESSIBILITY FEATURES ARE INCLUDED IN THIS SUBMITTAL.


THE PURPOSE OF THIS SUBMITTAL IS DOCUMENTATION OF EXISTING CONDITIONS ONLY.

HERNANDO COUNTY

3429 DELTONA BLVD SPRING HILL, FL. 34606

AL ABBADESSA

SUNRISE BAGEL

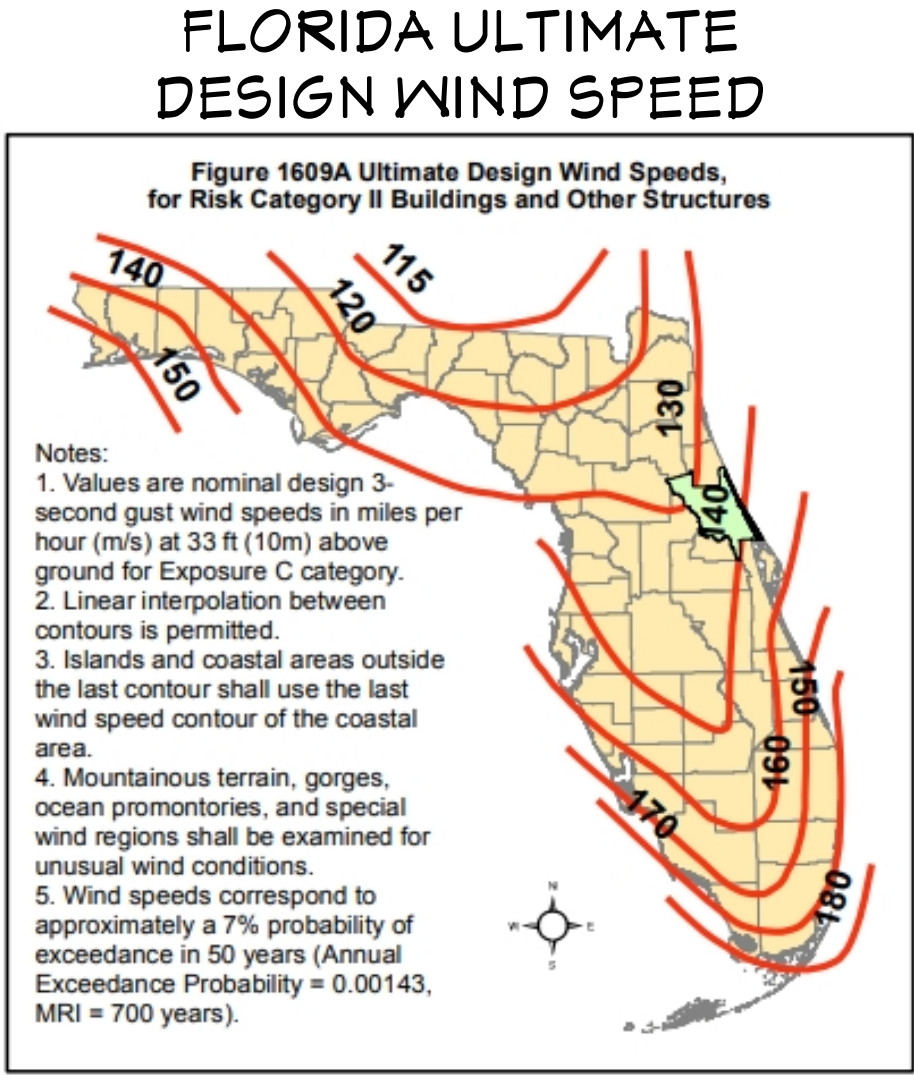

SOURCE: FLORIDA DEPARTMENT OF COMMUNITY AFFAIRS CODE STANDARDS DIVISION; APPLIED RESEARCH ASSOCIATES JUNE 28 2021 FLORIDA RESEARCH DATA

SITE INFORMATION:

CUSTOMER NAME:

AL ABBADESSA

PROJECT ADDRESS:

3429 DELTONA BLVD

SPRING HILL, FL. 34606

CUSTOMER PHONE NUMBER:

3527103932

CUSTOMER EMAIL:

HAROLDCABRERAUSA@GMAIL.COM

CONTRACTOR INFORMATION:

SEATING CONTRACTORS USA,
DBA: SMART CHOICE CONTRACTORS USA,
19815 STATE ROAD 52
LAND O LAKES Florida 34697
813-505-7560
CCC - 1505749
(813) 505-7650
PHIL@JUSTSMARTCHOICE.COM

OTHER DETAILS:

PROPERTY SEA LEVEL ELEV.: 38 FT.
PROPERTY GEO LOCATION CODES ARE:
28.4002° N LATITUDE
-82.4824° W LONGITUDE
ATC HAZARD ASCE 7-22
RISK CATEGORY: II
RENOVATION ESTIMATED VALUE:
0.00
YEAR BUILT 1995
LOT SIZE: 1,560.00 FT.

APPLICABLE GOVERNING CODES& NOTES:

SYSTEME SHALL BE INSTALL UNDER THE FOLLOWING CODE STANDARDS:

- 2020 NATIONAL ELECTRIC CODE (N.E.C)
- 2023 FBC BUILDING (8TH EDITION.)
- 2023 FBC RESIDENTIAL (8TH EDITION.)
- 2020 NATIONAL ELECTRICAL CODE (NFPA 70).
- 2023 FFGC FLORIDA PREVENTION CODE 8TH EDITION.

SITE SPECIFICATIONS:

CONSTRUCTION: SINGLE FAMILY DWELLING (SFD)
ZONING: RESIDENTIAL
NO. OF STORY: TWO STORY EXPOSURE
CATEGORY: B;
RISK CATEGORY: II
WIND SPEED (ASCE 7-22) : 140 MPH
GROUND SNOW LOAD (ASCE 7-22) : 0 Lb/Sqft
ASHRAE EXTREME LOW: 1°C
ASHRAE HIGH TEMP (2% AVG.): 34°C
ASHRAE DISTANCE ABOVE ROOF (7/8") : 56°
PARCEL ID: R32 323 17 5251 1786 0030
PROPERTY HEATED AREA SqFt.: 1,107
PROPERTY FULL AREA SqFt.: 1,107

SAT. VIEW



ARIAL VIEW



FRONT VIEW



This drawings are sole property of Seating Constructors USA, (DBA Smart Choice Contractors USA) Unless otherwise provided for by contract, or the writing means, the contents of this drawing are confidential & shall be not transmitted to any other party accepted and agreed by Smart Choice Contractors USA. 2025 Copyright .

SHEET TITLE		CUSTOMER NAME: AL ABBADESSA		CUSTOMER INFORMATION Email: HAROLDCABRERAUSA@GM Phone:AIL.COM3527103932			NICHOLSON ENGINEERING ASSOCIATES, INC.			REVISIONS			01
COVER PAGE		PROJECT ADDRESS: 3429 DELTONA BLVD SPRING HILL, FL. 34606		PROJECT OPEN DATE: JUN. 10. 2026			7468 Horse Lake Rd, Brooksville, FL 34601 Phone: 352.799.0170 Fax: 352.754.9167			DRAWINGS LATEST REMARKS			
										1 01.07.26 FLOOR PLAN DRAWINGS PERMIT SET.			
						2							
						3							
				PROJECT REVISED BY : MICHAEL D. JOHNSON				PROJECT NUMBER: 0024696		DESIGN DATE: 01.07.26		C	



NICHOLSON ENGINEERING ASSOCIATES, INC.

7468 Horse Lake Rd,
Brooksville, FL 34601
Phone: 352.799.0170
Fax: 352.754.9167



01

C

BAGEL RESTAURANT NOTES:

1 HANDWASHING SINK TO RAMIAN:
EXISTING HAND SINK TO REMAIN. HAND SINK LOCATION
COMPLIES WITH FLORIDA FOOD CODE §5-203.11 AND
DBPR REQUIREMENTS. NO CHANGES PROPOSED.

2 EXISTING COMMERCIAL KITCHEN EXHAUST HOOD:

EXISTING COMMERCIAL EXHAUST HOOD AND
ASSOCIATED EXHAUST SYSTEM. INSTALLATION
COMPLIES WITH THE FLORIDA MECHANICAL CODE 2023,
FLORIDA FIRE PREVENTION CODE, NFPA 96 STANDARD
FOR VENTILATION CONTROL AND FIRE PROTECTION OF
COMMERCIAL COOKING OPERATIONS, AND APPLICABLE
DBPR DIVISION OF HOTELS AND RESTAURANTS
REQUIREMENTS.

3 EXISTING ACCESSIBLE RESTROOM:

EXISTING ACCESSIBLE RESTROOM. RESTROOM LAYOUT,
FIXTURES, CLEARANCES, ACCESSIBLE ROUTE, TURNING
SPACE, DOOR CLEARANCES, GRAB BARS, LAVATORY,
WATER CLOSET, AND ACCESSORIES COMPLY WITH THE
FLORIDA ACCESSIBILITY CODE FOR BUILDING
CONSTRUCTION, 8TH EDITION (2023), ICC A111.1
ACCESSIBLE AND USABLE BUILDINGS AND FACILITIES,
THE AMERICANS WITH DISABILITIES ACT (ADA)
STANDARDS FOR ACCESSIBLE DESIGN, AND APPLICABLE
DBPR DIVISION OF HOTELS AND RESTAURANTS
REQUIREMENTS (INTRUSION RESISTANCE, AND FULL
CODE COMPLIANCE. (TYF.)

4 EXISTING FIRE EXTINGUISHER LOCATION:

EXISTING FIRE EXTINGUISHER LOCATION. FIRE
EXTINGUISHERS ARE PROVIDED AND LOCATED IN
ACCORDANCE WITH THE FLORIDA FIRE PREVENTION
CODE, 8TH EDITION (2023), NFPA 10 STANDARD FOR
PORTABLE FIRE EXTINGUISHERS, NFPA 101 LIFE SAFETY
CODE, AND APPLICABLE DBPR DIVISION OF HOTELS AND
RESTAURANTS REQUIREMENTS. FIRE EXTINGUISHERS
SHALL REMAIN READILY ACCESSIBLE AND LOCATED
ALONG REQUIRED PATHS OF EGRESS AS SHOWN ON THE
PLAN.

EXISTING FIRE EXTINGUISHER PROVIDED ADJACENT TO
EXIT DOOR. LOCATION COMPLIES WITH THE FLORIDA
FIRE PREVENTION CODE (2023), NFPA 10, NFPA 101 LIFE
SAFETY CODE, AND APPLICABLE DBPR REQUIREMENTS.
FIRE EXTINGUISHER IS LOCATED IN A VISIBLE AND
ACCESSIBLE LOCATION ALONG THE MEANS OF EGRESS
AS REQUIRED BY CODE

5 THREE-COMPARTMENT SINK:

EXISTING THREE-COMPARTMENT SINK PROVIDED IN
ACCORDANCE WITH THE FLORIDA FOOD CODE, CHAPTER
4, AND APPLICABLE DBPR DIVISION OF HOTELS AND
RESTAURANTS REQUIREMENTS FOR WAREWASHING
OPERATIONS.

6 MOP SINK:

EXISTING SERVICE SINK PROVIDED FOR JANITORIAL
OPERATIONS IN ACCORDANCE WITH THE FLORIDA FOOD
CODE AND APPLICABLE DBPR REQUIREMENTS.

7 WALK-IN COOLER / REFRIGERATION:

EXISTING COMMERCIAL REFRIGERATION EQUIPMENT
MAINTAINS FOOD STORAGE TEMPERATURES AS
REQUIRED BY THE FLORIDA FOOD CODE AND DBPR
REQUIREMENTS.

8 FOOD PREPARATION AREA:

EXISTING FOOD PREPARATION AREA PROVIDED WITH
REQUIRED HANDWASHING FACILITIES AND SANITARY
SURFACES IN ACCORDANCE WITH THE FLORIDA FOOD
CODE.

9 WATER HEATER:

EXISTING WATER HEATING EQUIPMENT PROVIDES HOT
WATER TO REQUIRED FIXTURES IN ACCORDANCE WITH
THE FLORIDA PLUMBING CODE AND FLORIDA FOOD CODE


10 HOOD FIRE SUPPRESSION SYSTEM:

EXISTING FIRE SUPPRESSION SYSTEM PROVIDED FOR
COMMERCIAL COOKING OPERATIONS IN ACCORDANCE
WITH NFPA 17A, NFPA 96, FLORIDA FIRE PREVENTION
CODE, AND APPLICABLE DBPR REQUIREMENTS.

11 EXISTING CUSTOMER SEATING AREA:

EXISTING CUSTOMER SEATING AREA PROVIDED WITH
ACCESSIBLE ROUTES AND ACCESSIBLE SEATING IN
ACCORDANCE WITH THE FLORIDA ACCESSIBILITY CODE
2023 AND ADA STANDARDS.

EXISTING FLOOR PLAN

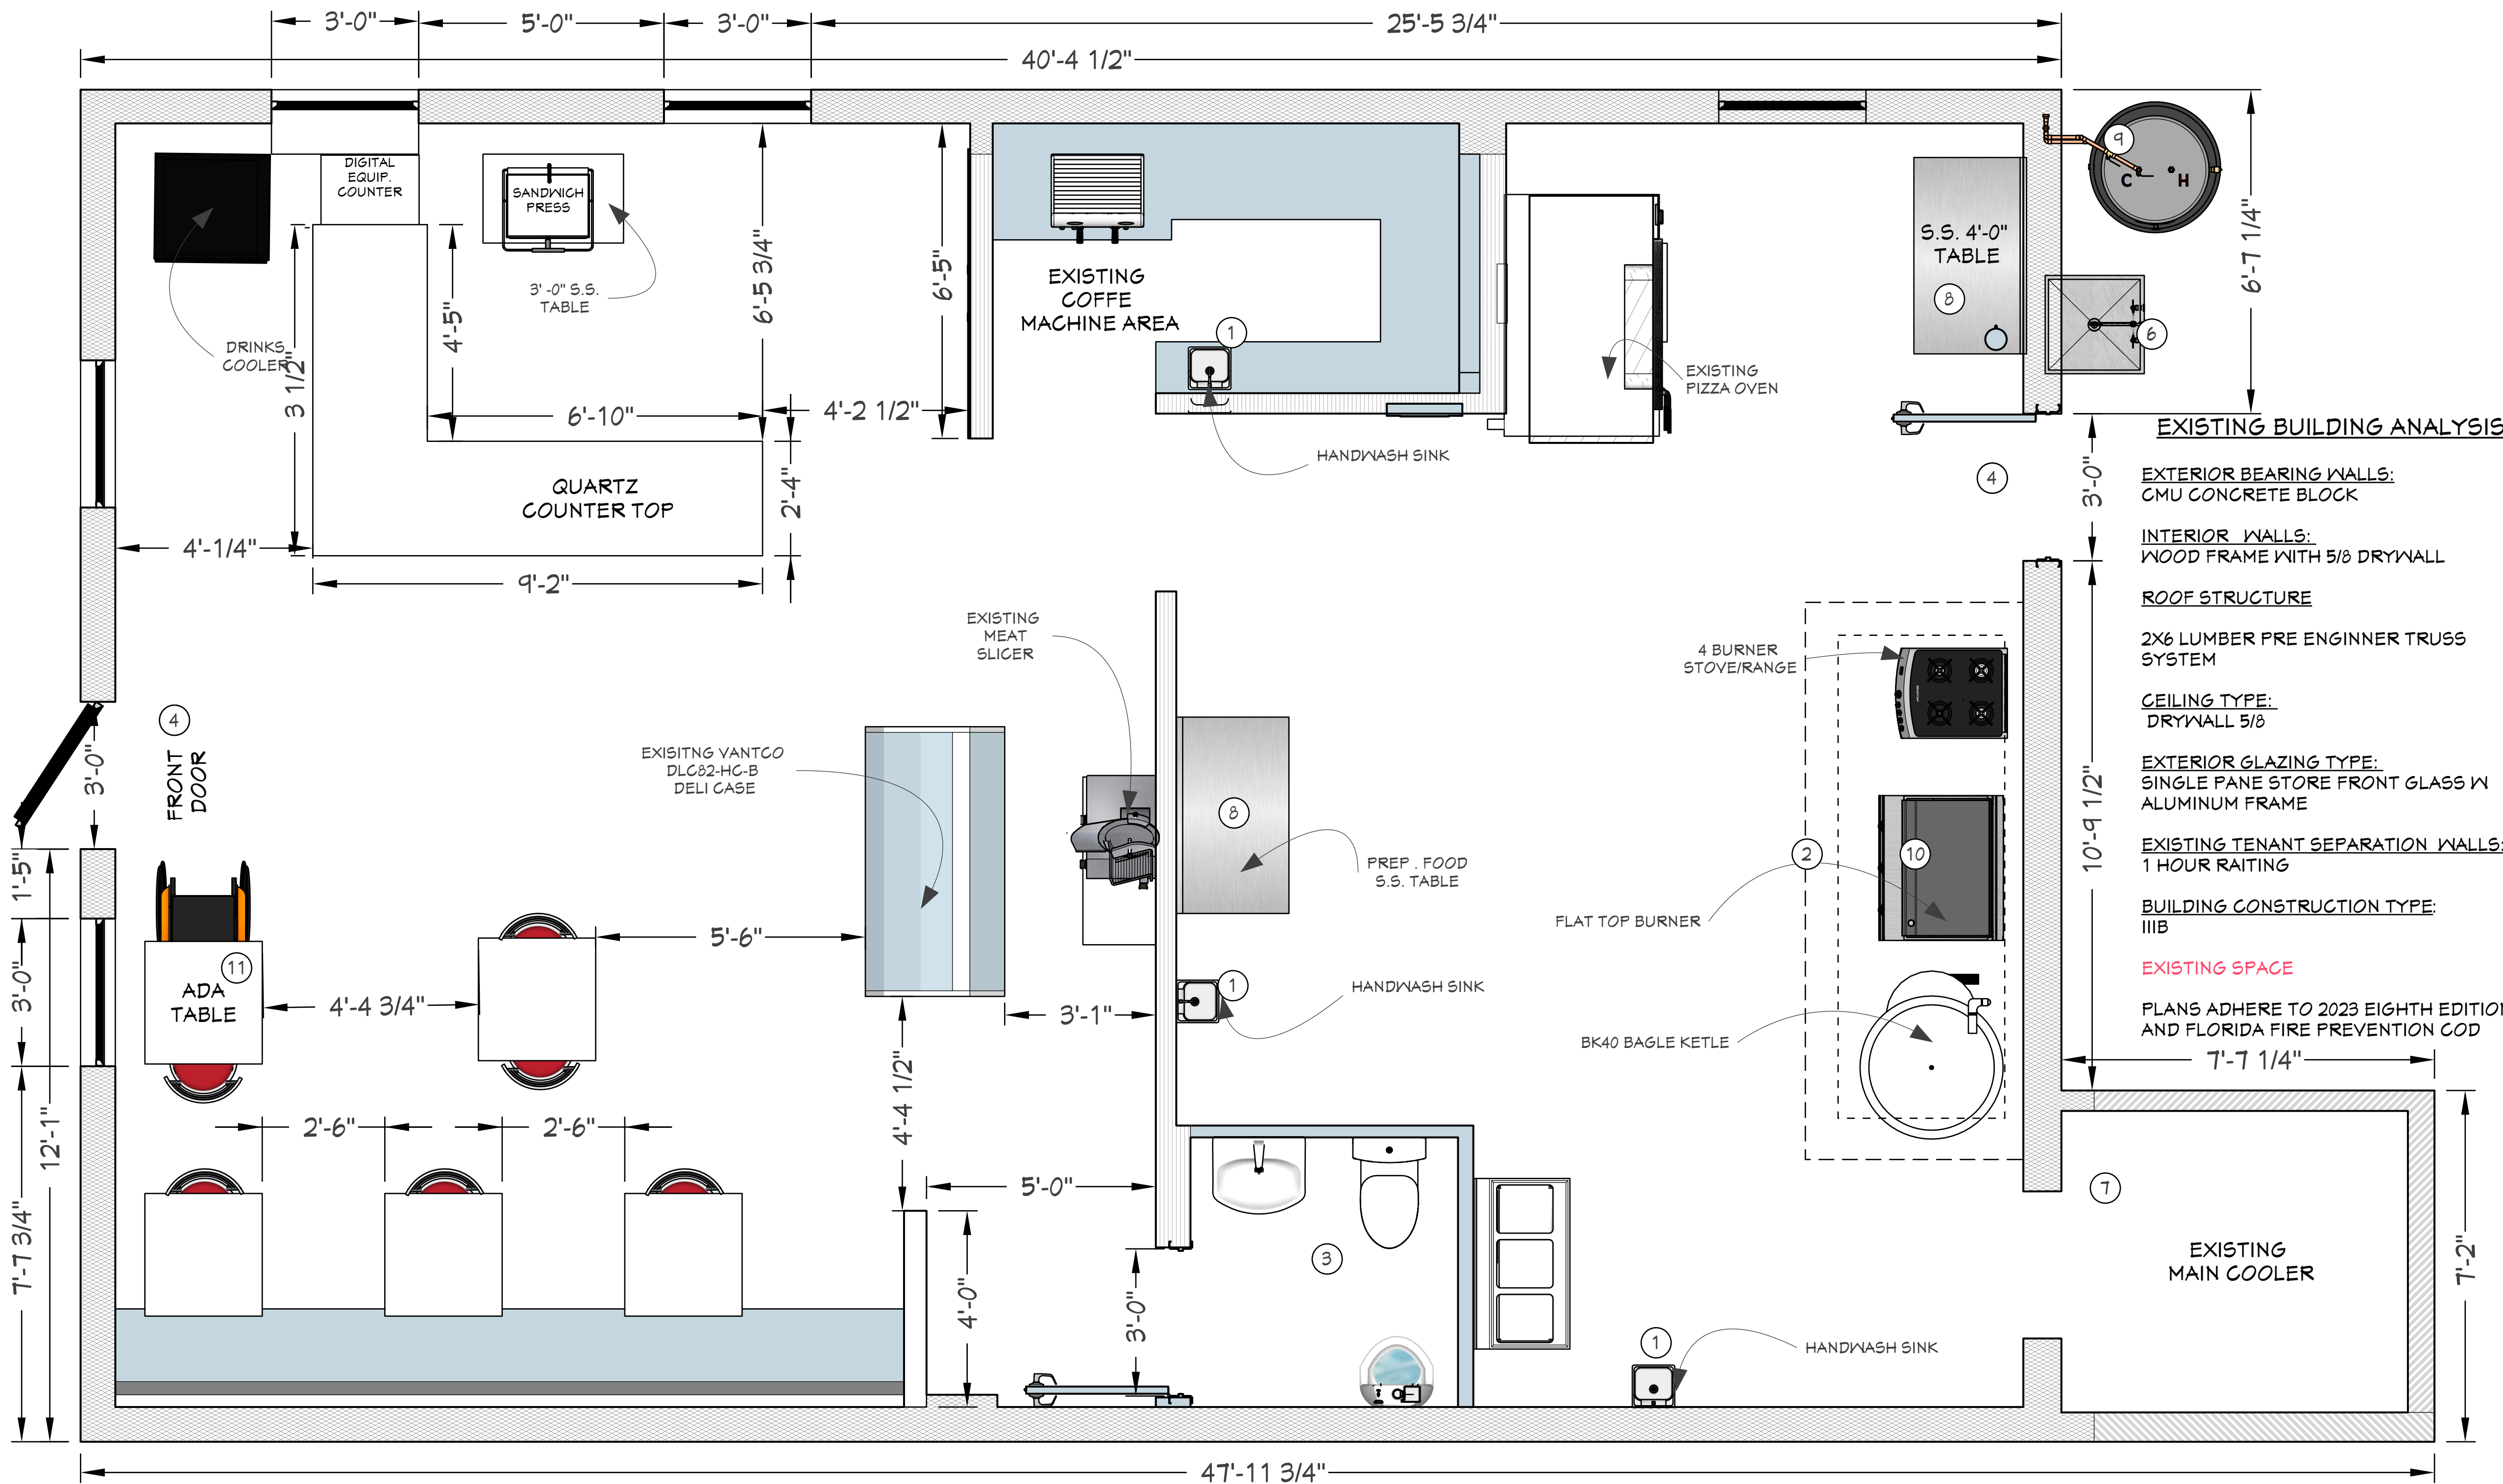

NEW FLOOR PLAN

CLASSIFICATION	OCCUPANCY	DESCRIPTION	WATER CLOSETS		LAVATORIES		DRINKING FOUNTAIN	OTHER
			MALE	FEMALE	MALE	FEMALE		
ASSEMBLY	A-2	BAGEL SHOP	1 PER 75		1 PER 75		1 PER 500	1 SERVICE SINK

This drawings are sole property of Seating Constructors USA, (DBA Smart Choice Contractors USA) Unless otherwise provided for by contract, or the writing means, the contents of this drawing are confidential & shall be not transmitted to any other party accepted and agreed by Smart Choice Contractors USA. 2025 Copyright .

SHEET TITLE

FLOOR PLAN

CUSTOMER NAME:

AL ABBADESSA

PROJECT ADDRESS:

3429 DELTONA BLVD
SPRING HILL, FL. 34606

CUSTOMER INFORMATION


Email: HAROLDCABRERAUSA@GM
Phone:AIL.COM3527103932

PROJECT OPEN DATE:

JUN. 10. 2026

PROJECT REVISED BY :

MICHAEL D. JOHNSON

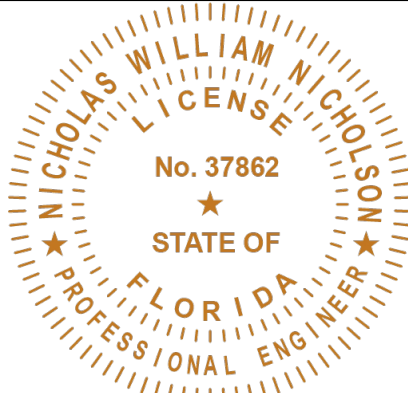

NICHOLSON ENGINEERING
ASSOCIATES, INC.

7468 Horse Lake Rd,
Brooksville, FL 34601
Phone: 352.799.0170
Fax: 352.754.9167




REVISIONS


	MM/DD/YY	DRAWINGS LATEST REMARKS
1	01.07.26	FLOOR PLAN DRAWINGS PERMIT SET.
2		
3		
PROJECT NUMBER: 0024696		DESIGN DATE: 01.07.26

A 02

LIFE SAFETY PLAN

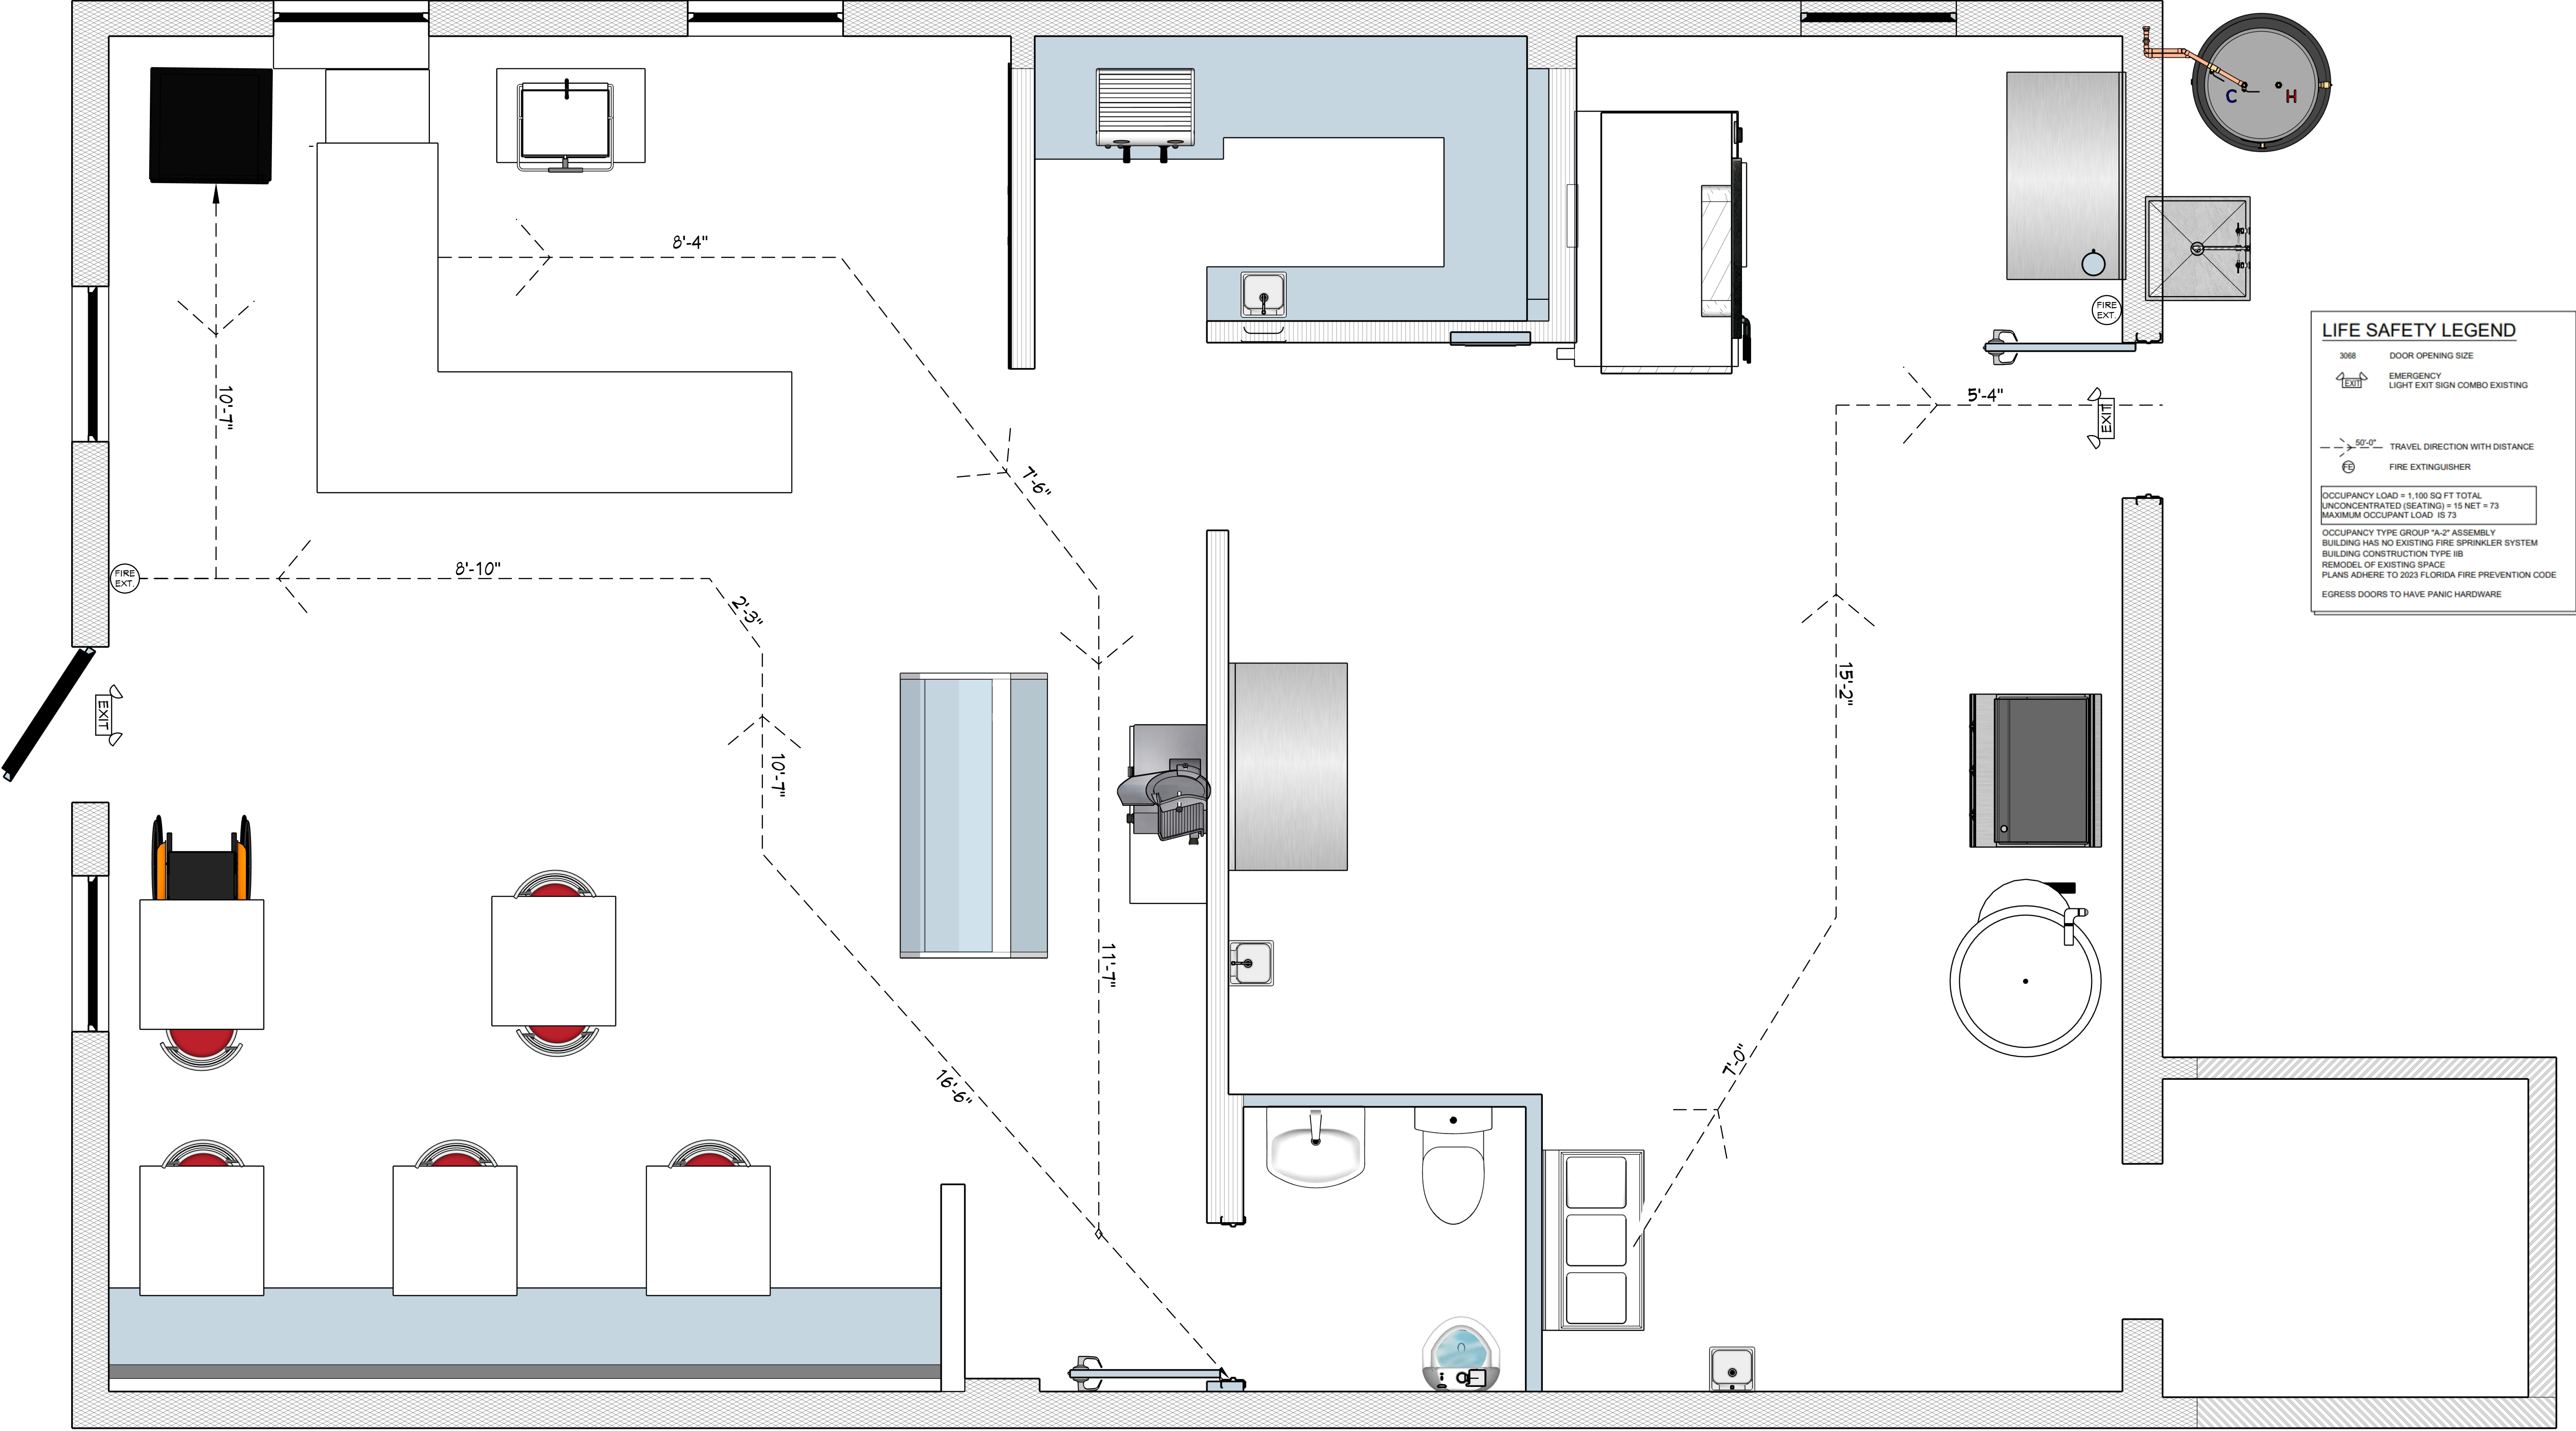

This drawings are sole property of Seating Constructors USA, (DBA Smart Choice Contractors USA) Unless otherwise provided for by contract, or the writing means, the contents of this drawing are confidential & shall be not transmitted to any other party accepted and agreed by Smart Choice Contractors USA. 2025 Copyright .

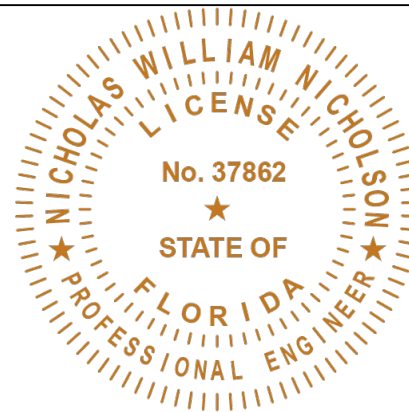SHEET TITLE		CUSTOMER NAME: AL ABBADESSA	CUSTOMER INFORMATION Email: HAROLDCABRERAUSA@GMAIL.COM Phone: AIL.COM35271103932			NICHOLSON ENGINEERING ASSOCIATES, INC. 7468 Horse Lake Rd, Brooksville, FL 34601 Phone: 352.799.0170 Fax: 352.754.9167		REVISIONS	
LIFE SAFETY PLAN		PROJECT ADDRESS: 3429 DELTONA BLVD SPRING HILL, FL. 34606	PROJECT OPEN DATE: JUN. 10. 2026	MM/DD/YY				DRAWINGS LATEST REMARKS	
		PROJECT REVISED BY : MICHAEL D. JOHNSON		1				01.07.26	FLOOR PLAN DRAWINGS PERMIT SET.
				2					
				3					
							PROJECT NUMBER: 0024696	DESIGN DATE: 01.07.26	

CUT SHEETS



Notes & Details

Attractively present your fresh cheese, meat, and other refrigerated deli items with the Avantco DLC82-HC-B 82" black curved glass refrigerated deli case! With a smooth, curved glass design, this contemporary case keeps contents sanitary while beautifully displaying them on nine epoxy-coated shelves. Crisp, internal LED lighting provides superior visibility for your products. Having a deli case is sure to boost your impulse sales, because customers can clearly see the products you're offering behind the strong, damage-resistant glass front. A durable black-coated steel exterior combines with the painted aluminum and 304 stainless steel interior for long-lasting durability.

For optimal temperature retention, this deli case features foamed-in-place polyurethane insulation that protects the integrity of your refrigerated goods. A 4/5 hp compressor keeps the unit operating at temperatures between 33-40 degrees Fahrenheit, while circulating R290 refrigerant. This specialized refrigerant has an ozone depletion potential (ODP) of 0 and a global warming potential (GWP) of 3. The digital temperature controller ensures quick temperature readability, and for convenience, the unit has an auto defrost function. This deli case uses gravity coil refrigeration, meaning it is able to keep product cold, fresh, and ready to serve without the risk of dehydration. A 115V electrical connection is required for operation.

WARNING: This product can expose you to chemicals including lead, which are known to the State of California to cause cancer and birth defects or other reproductive harm. For more information, go to www.cdswarning.com.

Avantco Refrigeration



Item #: 178DLCB2HC8 Project: _____
Qty: _____ Date: _____ Approval: _____

Avantco DLC82-HC-B 82" Black Curved Glass Refrigerated Deli Case

Item #178DLCB2HC8



Technical Data

Width	82 inches
Depth	32 1/2 inches
Height	42 7/8 inches
Power Cord Length	98 inches
Bottom Shelf Width	25 3/8 inches
Interior Width	78 inches
Left Door Opening Width	25 5/8 inches
Middle Door Opening Width	25 5/8 inches
Middle Shelf Width	24 7/16 inches
Right Door Opening Width	25 5/8 inches

Features

- Curved glass front and LED lighting to best showcase fresh deli product
- Durable black exterior with a 2 1/2" deep countertop for convenient workspace
- Nine epoxy-coated shelves; six are adjustable to accommodate different-sized products
- Digital controller for easy operation and automatic defrost for easy maintenance
- Uses R290, 4/5 hp; 115V

Certifications




Avantco Refrigeration

Technical Data



Top Shelf Width	25 9/16 inches
Bottom Shelf Depth	24 13/16 inches
Interior Depth	26 3/4 inches
Middle Shelf Depth	22 7/16 inches
Top Shelf Depth	20 1/2 inches
Interior Height	26 3/4 inches
Amps	5 Amps
Hertz	40 Hz
Phase	1 Phase
Voltage	115 Volts
Wattage	518 Watts
BTU (LBP)	2040 BTU
Capacity	28.1 cu. ft.
Color	Black
Compressor Location	Bottom Mounted
Display Case Type	Refrigerated Single Duty
Door Style	Sliding
Features	LED Lighting Lighted Interior
Glass Style	Curved
Horsepower	4.5 hp
Installation Type	Floor Model
Number of Doors	3 Doors
Number of Shelves	9 Shelves
Number of Tiers	3 Tiers
Plug Type	NEMA 5-15P
Refrigerant Capacity	4.9 oz.
Refrigerant Type	R-290
Refrigeration Type	Gravity Coil
Service Type	Full Service
Starting Amps	15 Amps
Starting Wattage	1554 Watts
Temperature	33 - 40 Degrees F
Type	Deli Cases

Plan View

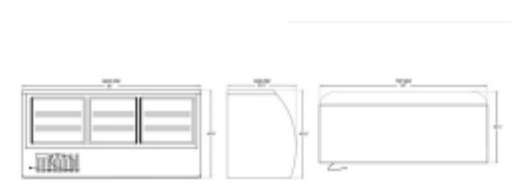

BLODGETT

981/951 DECK OVEN

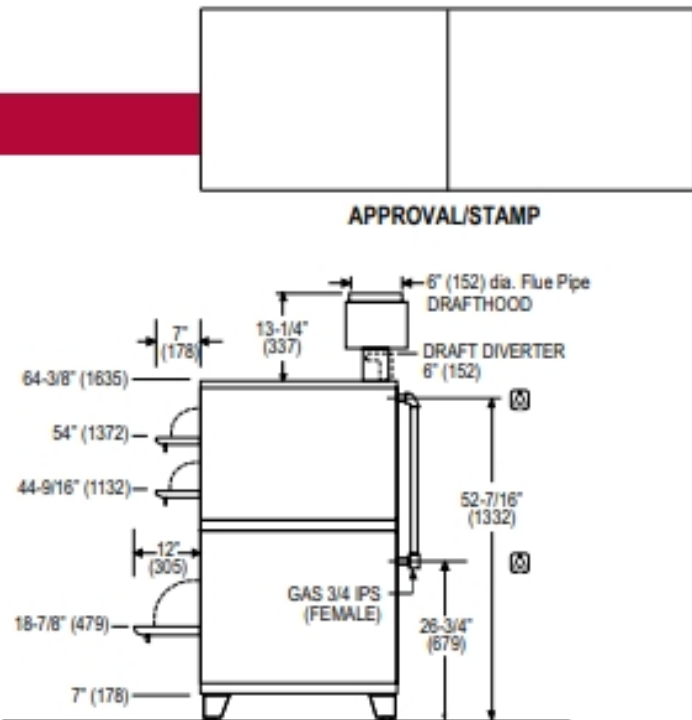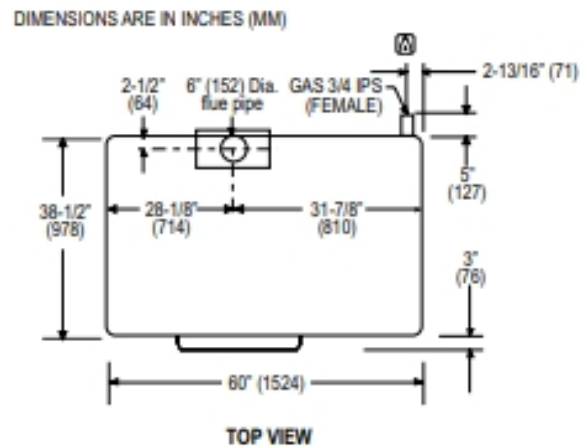

SHORT FORM SPECIFICATIONS Provide Blodgett combination deck oven, model 981/951. Each unit shall be a combination of two independent ovens (for a total of three baking compartments) with single, manifolded gas connections and flues. Construction shall be welded stainless steel top, front, back and sides, and shall be fully insulated on all sides. Ovens shall be supported by 7" high formed adjustable legs. Doors shall be counterbalanced (no springs) with concealed hinges and chrome plated tubular steel handles. Separate burner door provided for ignition, cleaning and adjustment. The upper section baking compartments (two) shall be 42" W x 7" H x 32" D each; the lower section baking compartment shall be 42" W x 12" H x 32" D. All shall be lined with aluminized steel, and decks shall be of 1/4 gauge press-formed, reinforced and flanged steel. Each section shall be gas heated by a free-floating, easily removable, duplex-type burner controlled by a liquid pressure thermostat with range of 200°F to 500°F. Provide with two year parts and one year labor warranty. Provide with options and accessories as indicated.

DIMENSIONS

Floor space 60" (1524mm) wide x 40" (1016mm) deep
Cooking Compartment (per section)
Top section (2) 42" (1067mm) W x 7" (178mm) H x 32" (813mm) D
Bottom section 42" (1067mm) W x 12" (305mm) H x 32" (813mm) D
Area per section 9.34 sq. ft. (0.87m²)
Total area 28.02 sq. ft. (2.6m²)

SECTION DETAILS

Number of section 2
Number of controls 2
Number of compartments 3

PRODUCT CLEARANCE

From combustible and non-combustible construction 6" (152 mm)

PAN CAPACITIES

10" (254mm) pie tins 36
18" x 26" (457mm x 660mm) bun pans 6
9-1/2" x 5" (241mm x 127mm) bread pans 72
9" x 7" (228mm x 178mm) roll pans 42
19" x 4" (483mm x 102mm) pullman pans 42
13" x 16-1/2" (330mm x 419mm) cup tins 27
20" x 28" (508mm x 711mm) roast pans 6
No. 200 pans (324mm x 527mm) 12
#1 bean pot 105
#2 bean pot 60
#3 bean pot 36
25 lb (11 kg) turkeys 5

GAS SUPPLY (per section)

3/4" NPT
Inlet Pressure
Natural Gas 7.0" W.C. min. - 10.5" W.C. max.
Propane 11.0" W.C. min. - 13.0" W.C. max.
Manifold Pressure
Natural Gas 5" W.C.
Propane 10" W.C.

MAXIMUM INPUT

951 38,000 BTU/hr
981 50,000 BTU/hr
951/981 88,000 BTU/hr

MINIMUM ENTRY CLEARANCE

Uncrated 32-1/2" (826mm)
Crated 37" (940mm)

SHIPPING INFORMATION

Approx. Weight
951 600 lbs. (272kg)
981 715 lbs. (324kg)
951/981 1315 lbs. (596kg)
Crate Sizes
65" (1651mm) x 37" (940mm) x 46.5" (1181mm)
#1 bean pot 105
#2 bean pot 60
#3 bean pot 36
25 lb (11 kg) turkeys 5

FOR COMMERCIAL USE ONLY

BLODGETT

981/951

Double Gas Deck Oven



OPTIONS AND ACCESSORIES

- (AT ADDITIONAL CHARGE)
■ Flexible gas hose with quick disconnect and restraining device
 - 36" (914 mm)
 - 48" (1219mm)
- QHT Rokite deck 1-1/2" (38.1mm) thick pizza type deck for 951 and 981 (bottom deck only)
- Steam jets
- FDT 300° to 650° temperature thermostat

OPTIONS AND ACCESSORIES (AT NO ADDITIONAL CHARGE)
□ Centigrade dial, 100°C to 300°C

Project _____
Item No. _____
Quantity _____

Ovens consist of basic sections and are a complete and separate unit capable of operating alone or in combination. All data is shown per oven section, unless otherwise indicated.

Refer to operator manual specification chart for listed model names.

EXTERIOR CONSTRUCTION

- Full angle iron frame
- Stainless steel front, top, sides and back
- Counterbalanced doors with concealed hinges
- Heavy chrome plated tubular steel door handle
- 7" (178mm) stainless steel legs are adjustable for leveling
- Burner doors open easily for ignition, cleaning or adjustment, without removal of any fastenings
- Vitreous fiber insulation at top, back, sides, bottom and doors.

INTERIOR CONSTRUCTION

- (1 - 981) 42" x 32" x 7" (1067mm x 813mm x 178mm) (1 - 951) 42" x 32" x 12" (1067mm x 813mm x 305mm) oven compartment interior
- Aluminized steel baking compartment liner
- Aluminized steel combustion chamber
- Steel deck supported by an angle iron frame
- 12 gauge (3.02mm) press-formed, reinforced and flanged aluminized steel deck

OPERATION

- Free-floating, easily removable duplex-tube burner
- Removable fixed orifices on main and pilot burner
- Main gas valve, temperature control valve and safety pilot valve fully within section body and are accessible through a covered and ventilated compartment in front.
- Air mixers with adjustable air shutters and locking device
- Liquid pressure thermostat with temperature control range of 200°F (93°C) to 500°F (288°C)

STANDARD FEATURES

- Fahrenheit dial 200°F to 500°F
- Vent kit
- Large crown angle trim
- Double connector for stacking
- Steel oven deck
- Two year parts and one year labor warranty
- Five year limited oven door warranty*

* For all international markets, contact your local distributor.


NOTE: The company reserves the right to make substitutions of components without prior notice



www.blodgett.com
42 Allen Martin Drive, Essex Junction, VT 05452
Phone: (802) 658-6600 | Fax: (802) 864-0183

P/N 35036 Rev 1 (4/19)

981/951 - DOUBLE

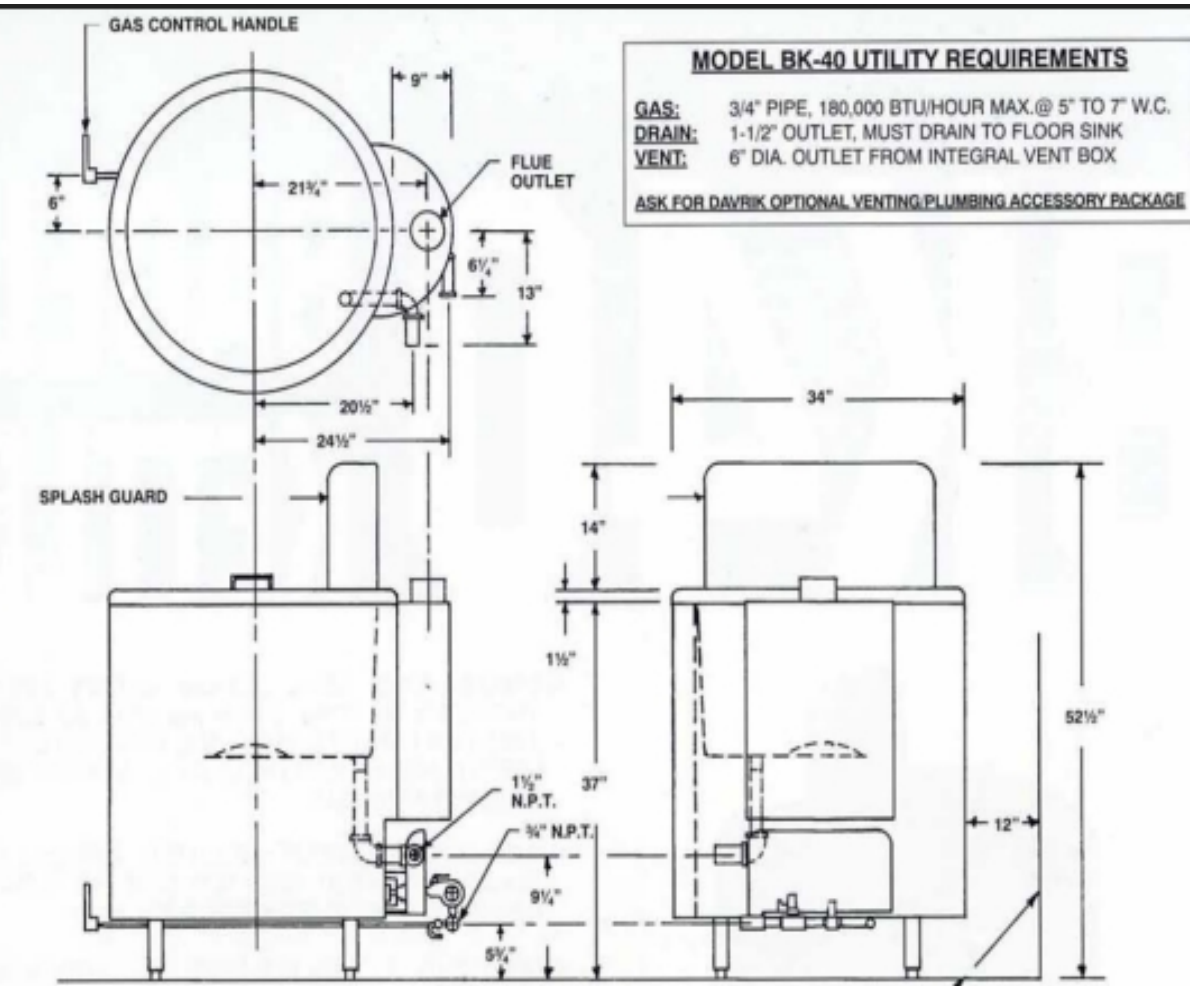

VENTING REQUIREMENTS

THE DAVRIK BK-40 BAGEL KETTLE IS SUPPLIED WITH A 6" VERTICAL COLLAR CONNECTION FOR THE FLUE OUTLET. A HEAVY WALL STAINLESS STEEL DRAFT DIVERTER IS INCLUDED. KETTLE IS TO BE INSTALLED UNDER AN APPROVED EXHAUST HOOD; THE FLUE VENT STACK IS TO VENT INTO THE CANOPY HOOD ONLY. DO NOT EXHAUST THE FLUE STACK INDEPENDENTLY. NOTE: ALL VENTING DETAILS MUST BE IN COMPLIANCE WITH LOCAL CODES.

OPTIONAL

PLUMBING AND VENTING PACKAGE, DESIGNED TO ASSIST THE INSTALLATION, THIS PACKAGE INCLUDES A KETTLE FILL FAUCET WITH MOUNTING BRACKET, 1-1/2" HIGH QUALITY BRASS DRAIN VALVE, AND 5 FOOT SECTION OF VENT PIPE WITH VENT PIPE SAFETY INSULATION WRAP.



Food Makers Bakery Equipment

16019 Adelante Street • Irwindale, CA 91702
Phone: (626) 358-1343 Fax: (626) 334-9970

Sales@fmebakery.com

INSTALLATION

THE BK-40 IS SHIPPED FULLY ASSEMBLED FOR EASY INSTALLATION. ALL COMPONENTS ARE FACTORY TESTED. ADJUSTABLE LEGS ARE PROVIDED FOR LEVELING ON UNEVEN FLOORS. CAUTION: TO REDUCE THE RISK OF FIRE, THE KETTLE IS TO BE MOUNTED ON NON-COMBUSTIBLE FLOORING THAT EXTENDS AT LEAST 12 INCHES BEYOND THE EQUIPMENT ON ALL SIDES. AT LEAST 12 INCHES OF HORIZONTAL SPACING MUST BE MAINTAINED BETWEEN THE KETTLE AND ANY COMBUSTIBLE WALLS, STRUCTURES OR MATERIALS. IMPORTANT: DO NOT ROUTE ANY UTILITIES (WIRING OR PLUMBING) WITHIN 12 INCHES OF THE KETTLE.

SHIPPING

CRATE DIMENSIONS: 41" X 49" X 49"
SHIPPING WEIGHT: 525 LBS. CLASS 85

BK40 BAGEL KETTLE



- UNIQUE SPUN BOWL DESIGN ALLOWS HEAT TRANSFER ON BOWL SIDES, AS WELL AS BOTTOM, FOR FASTER BOILING AND GREATER EFFICIENCY AND GAS SAVINGS OF HUNDREDS OF DOLLAR ANNUALLY.
- CONVENIENT, FRONT MOUNTED CONTROLS ALLOW OPERATOR GREATER CONTROL COMPARED TO ANY OTHER BAGEL KETTLE.
- SPUN BOWL DESIGN IS EASIER TO CLEAN THAN ANY OTHER KETTLE. THIS DESIGN IS BISCC APPROVED AND MEETS NSF CONSTRUCTION STANDARDS. NO OTHER TRADITIONAL BAGEL KETTLE IS SANITATION APPROVED
- NO ELECTRIC REQUIREMENTS AND AN IMPROVED, ACA CERTIFIED VENT SYSTEM WILL SAVE HUNDREDS OF DOLLARS IN CONSTRUCTION AND INSTALLATION COSTS.
- QUALITY, HIGH EFFICIENCY BURNER IS ADJUSTABLE FROM 80,000 TO 180,000 BTU'S PER HOUR.

THE NEW DAVRIK BK-40 BAGEL KETTLE HAS BEEN PERFECTED BY BAGEL BAKERS, FOR BAGEL BAKERS. IN PRODUCTION FOR OVER 20 YEARS, IT HAS ALL THE FEATURES AND REFINEMENTS NEEDED IN TODAY'S BAGEL BAKERY.

WHETHER YOU ARE MAKING THE TRADITIONAL EAST COAST BAGEL OR THE SOFT AND CHEWY WEST COAST BAGEL, YOU WILL BOIL PERFECT BAGELS EVERY TIME.

FOR SPEED, CONVENIENCE, GAS EFFICIENCY, AND SANITATION, THERE IS NO COMPARISON. THE ONLY FULLY APPROVED AMERICAN GAS ASSOCIATION (AGA) AND BAKERY SANITATION (BISCC) CERTIFIED BAGEL KETTLE AVAILABLE TODAY!



Food Makers Bakery Equipment

16019 Adelante Street • Irwindale, CA 91702
Phone: (626) 358-1343 Fax: (626) 334-9970

www.FMBE.com

This drawings are sole property of Seating Constructors USA, (DBA Smart Choice Contractors USA) Unless otherwise provided for by contract, or the writing means, the contents of this drawing are confidential & shall be not transmitted to any other party accepted and agreed by Smart Choice Contractors USA. 2025 Copyright .

SHEET TITLE

CUT SHEETS

CUSTOMER NAME:

AL ABBADESSA

PROJECT ADDRESS:

3429 DELTONA BLVD
SPRING HILL, FL. 34606

CUSTOMER INFORMATION


Email: HAROLDCABRERAUSA@GM
Phone:AIL.COM3527103932

PROJECT OPEN DATE:

JUN. 10. 2026

PROJECT REVISED BY :

MICHAEL D. JOHNSON

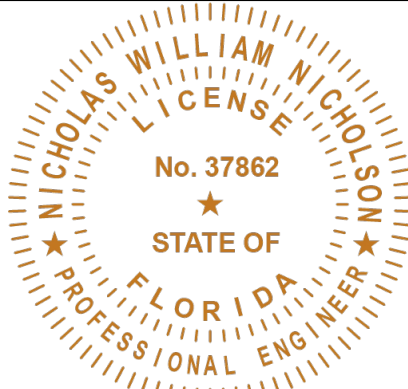

NICHOLSON ENGINEERING ASSOCIATES, INC.

7468 Horse Lake Rd,
Brooksville, FL 34601
Phone: 352.799.0170
Fax: 352.754.9167







REVISIONS

	MM/DD/YY	DRAWINGS LATEST REMARKS
1	01.07.26	FLOOR PLAN DRAWINGS PERMIT SET.
2		
3		
PROJECT NUMBER: 0024696		DESIGN DATE: 01.07.26

A 04

ISO DETAILS

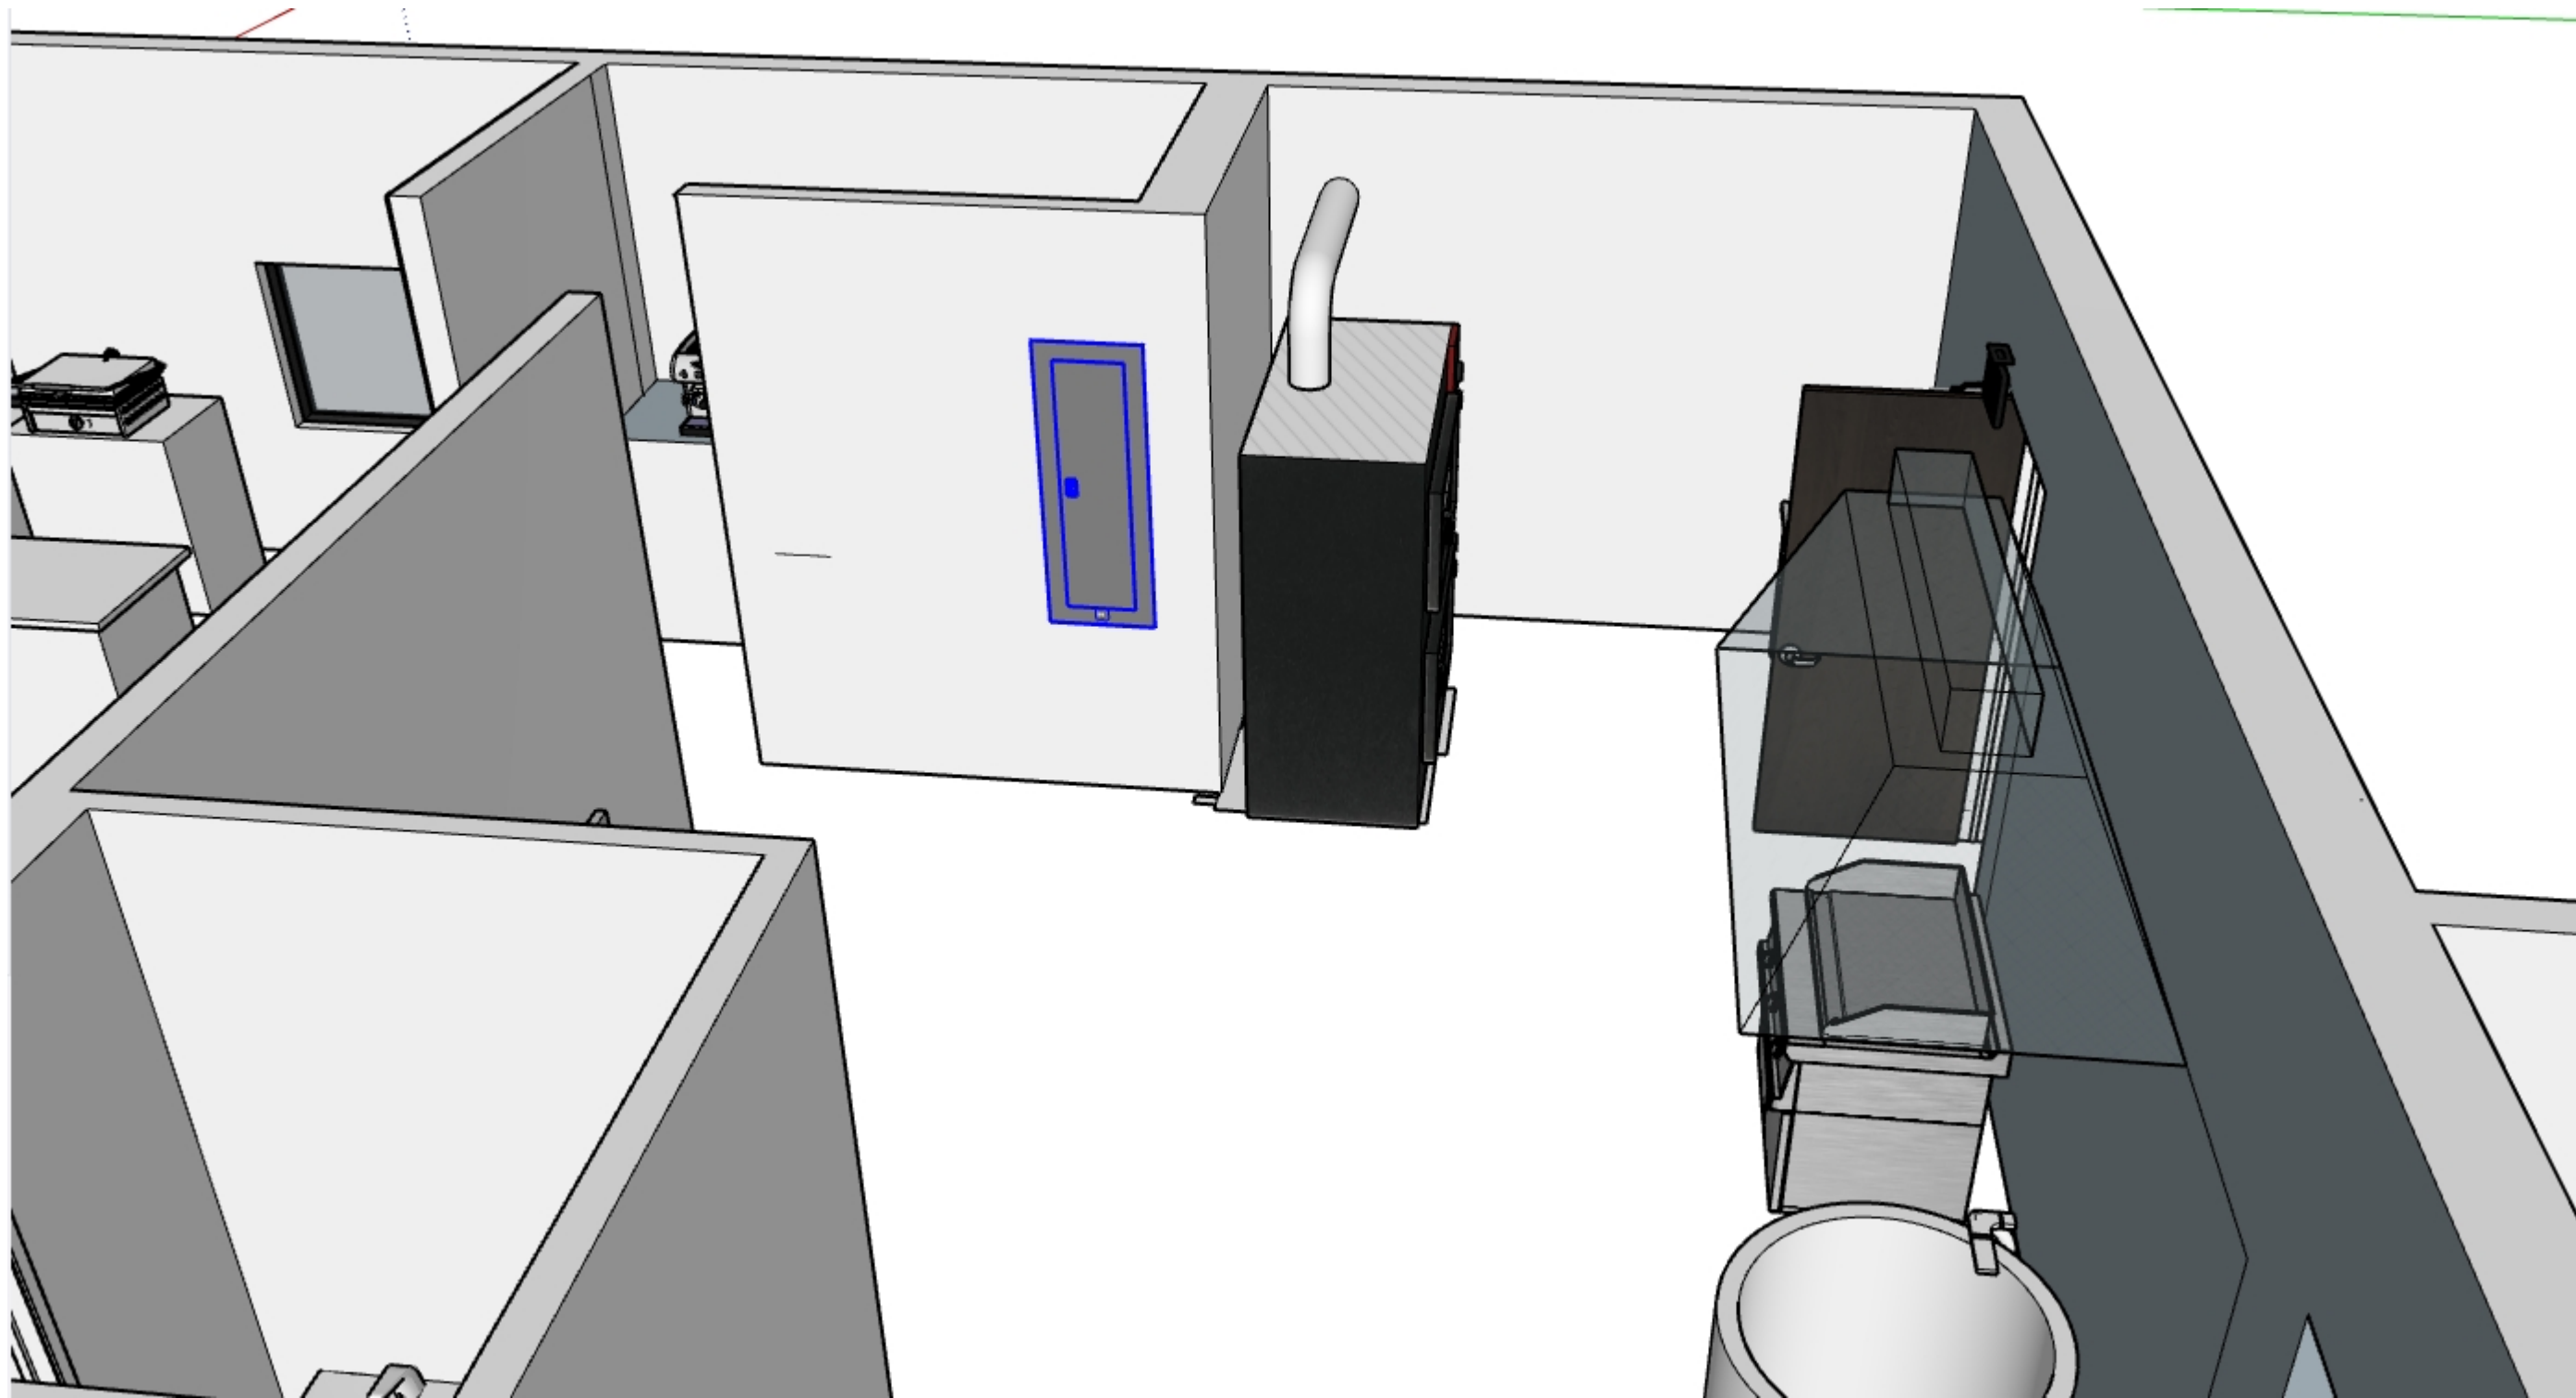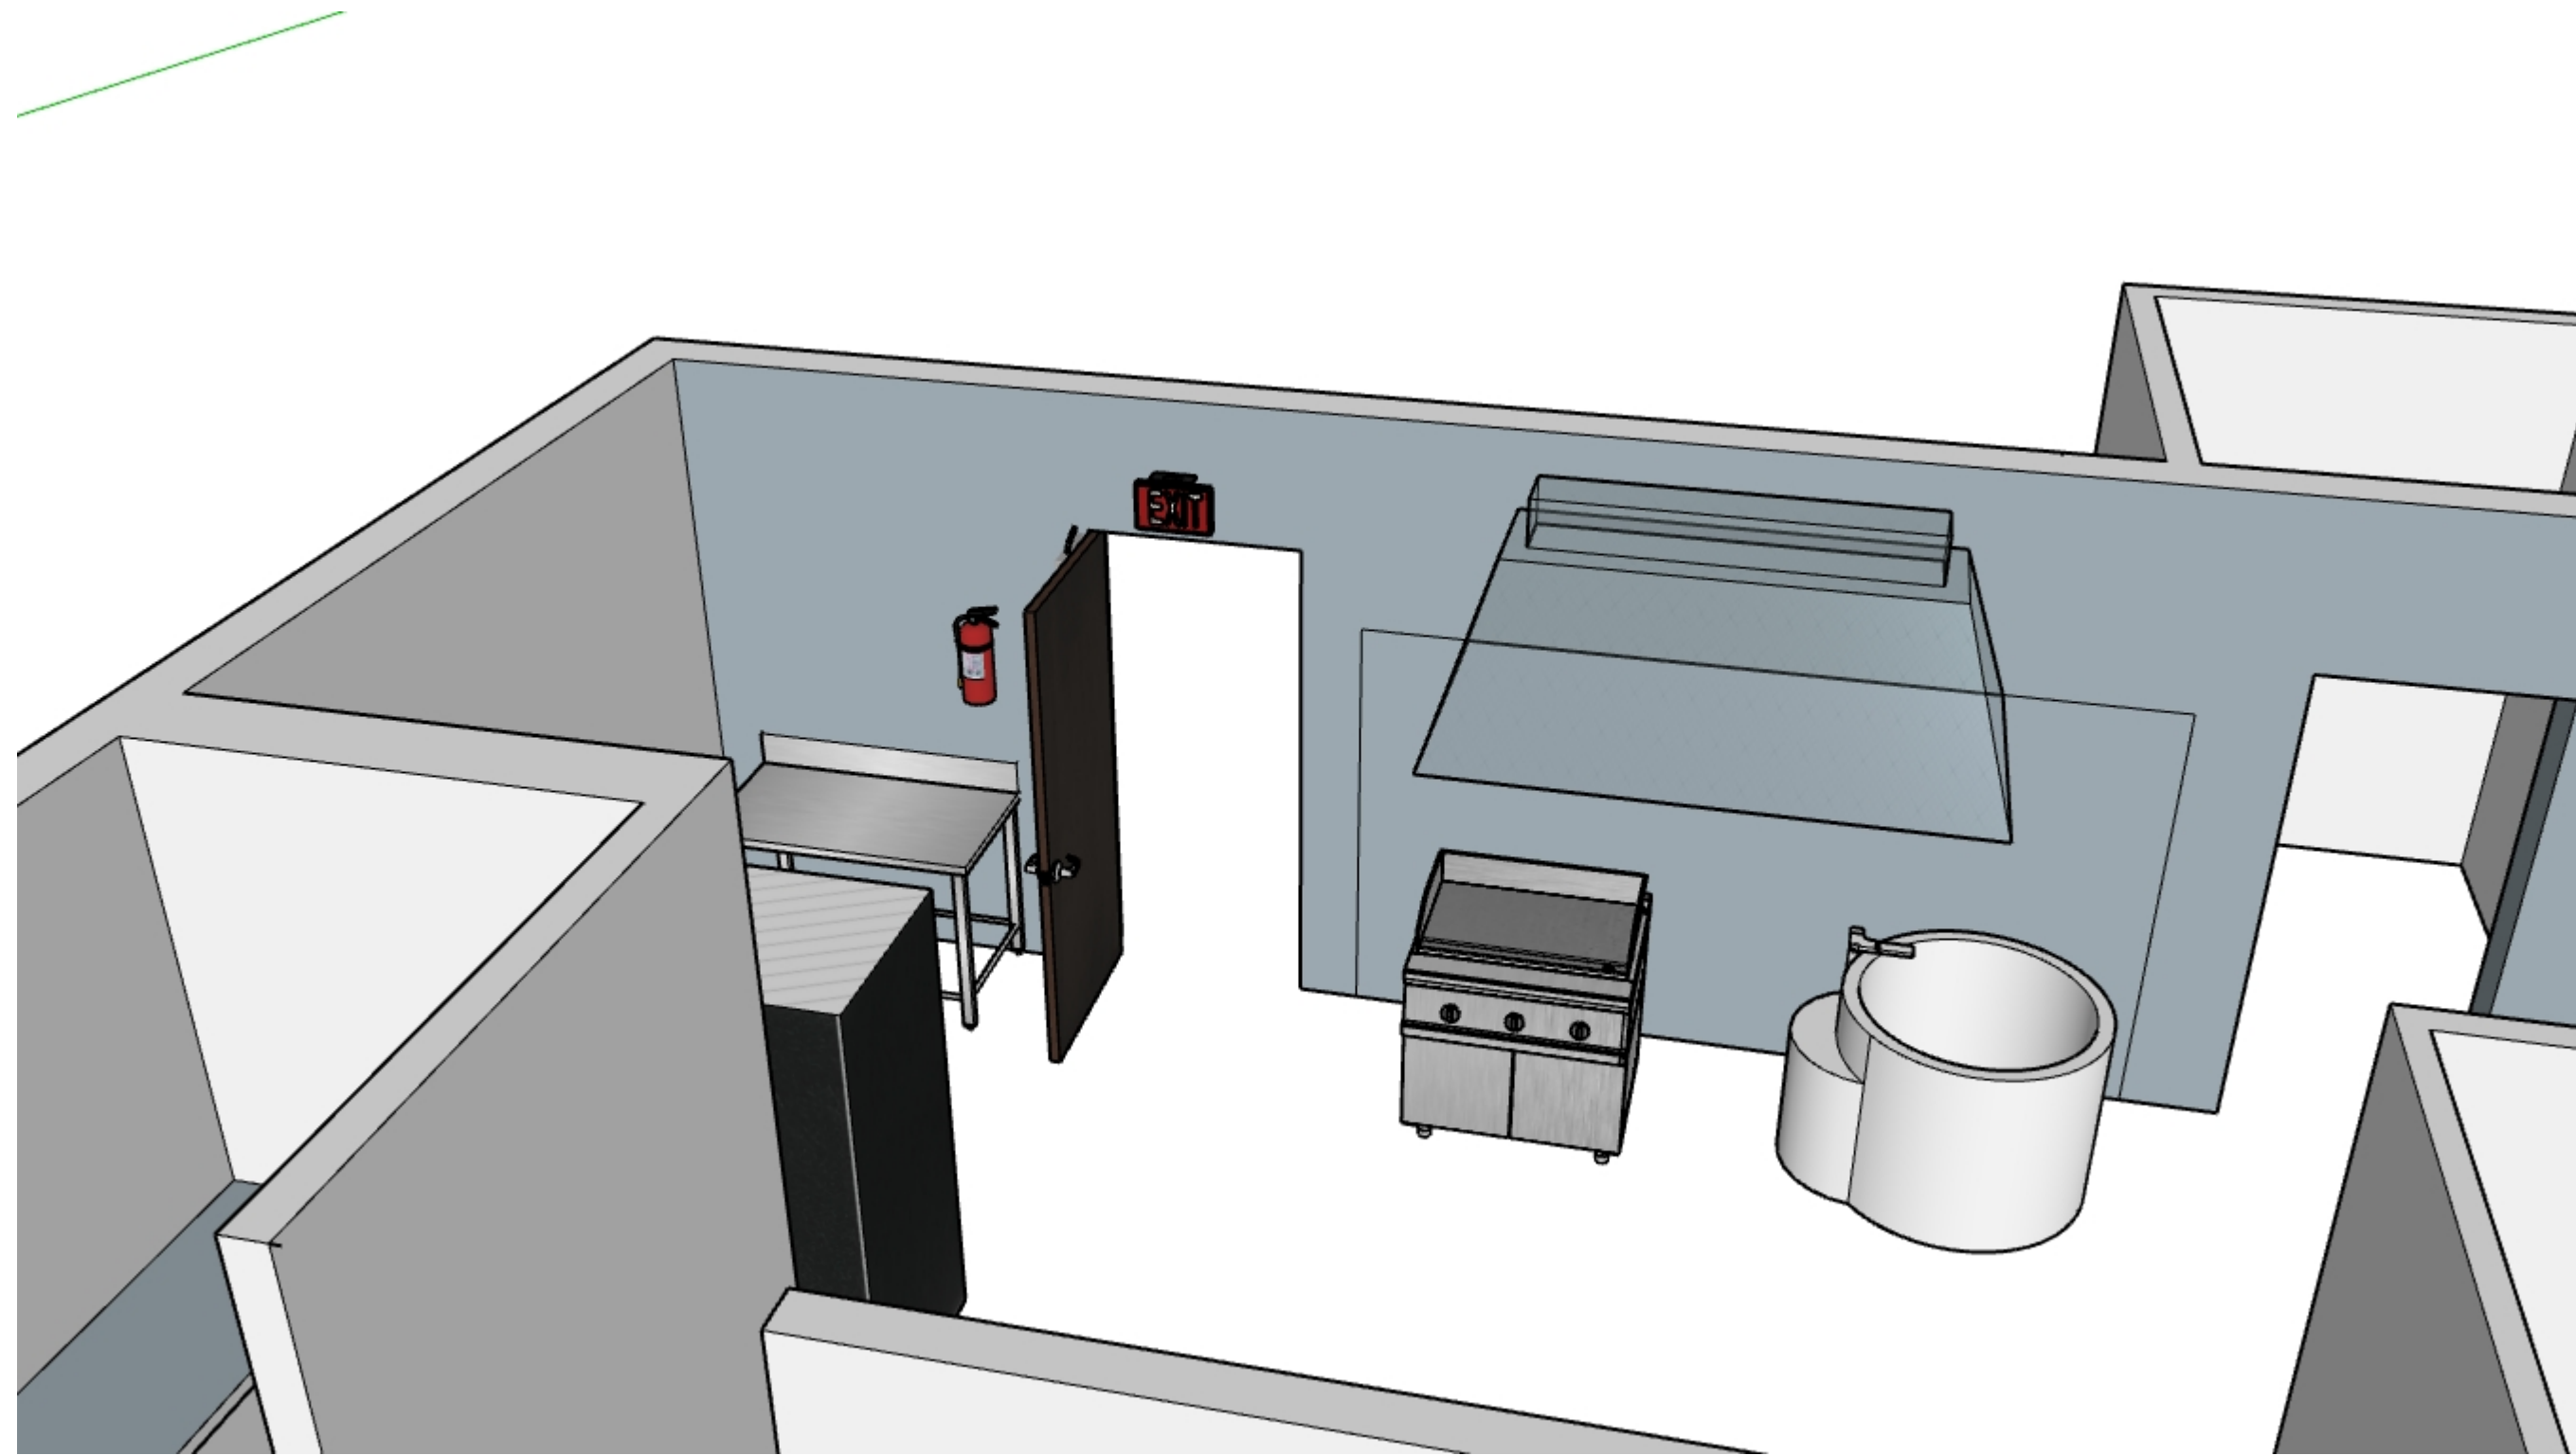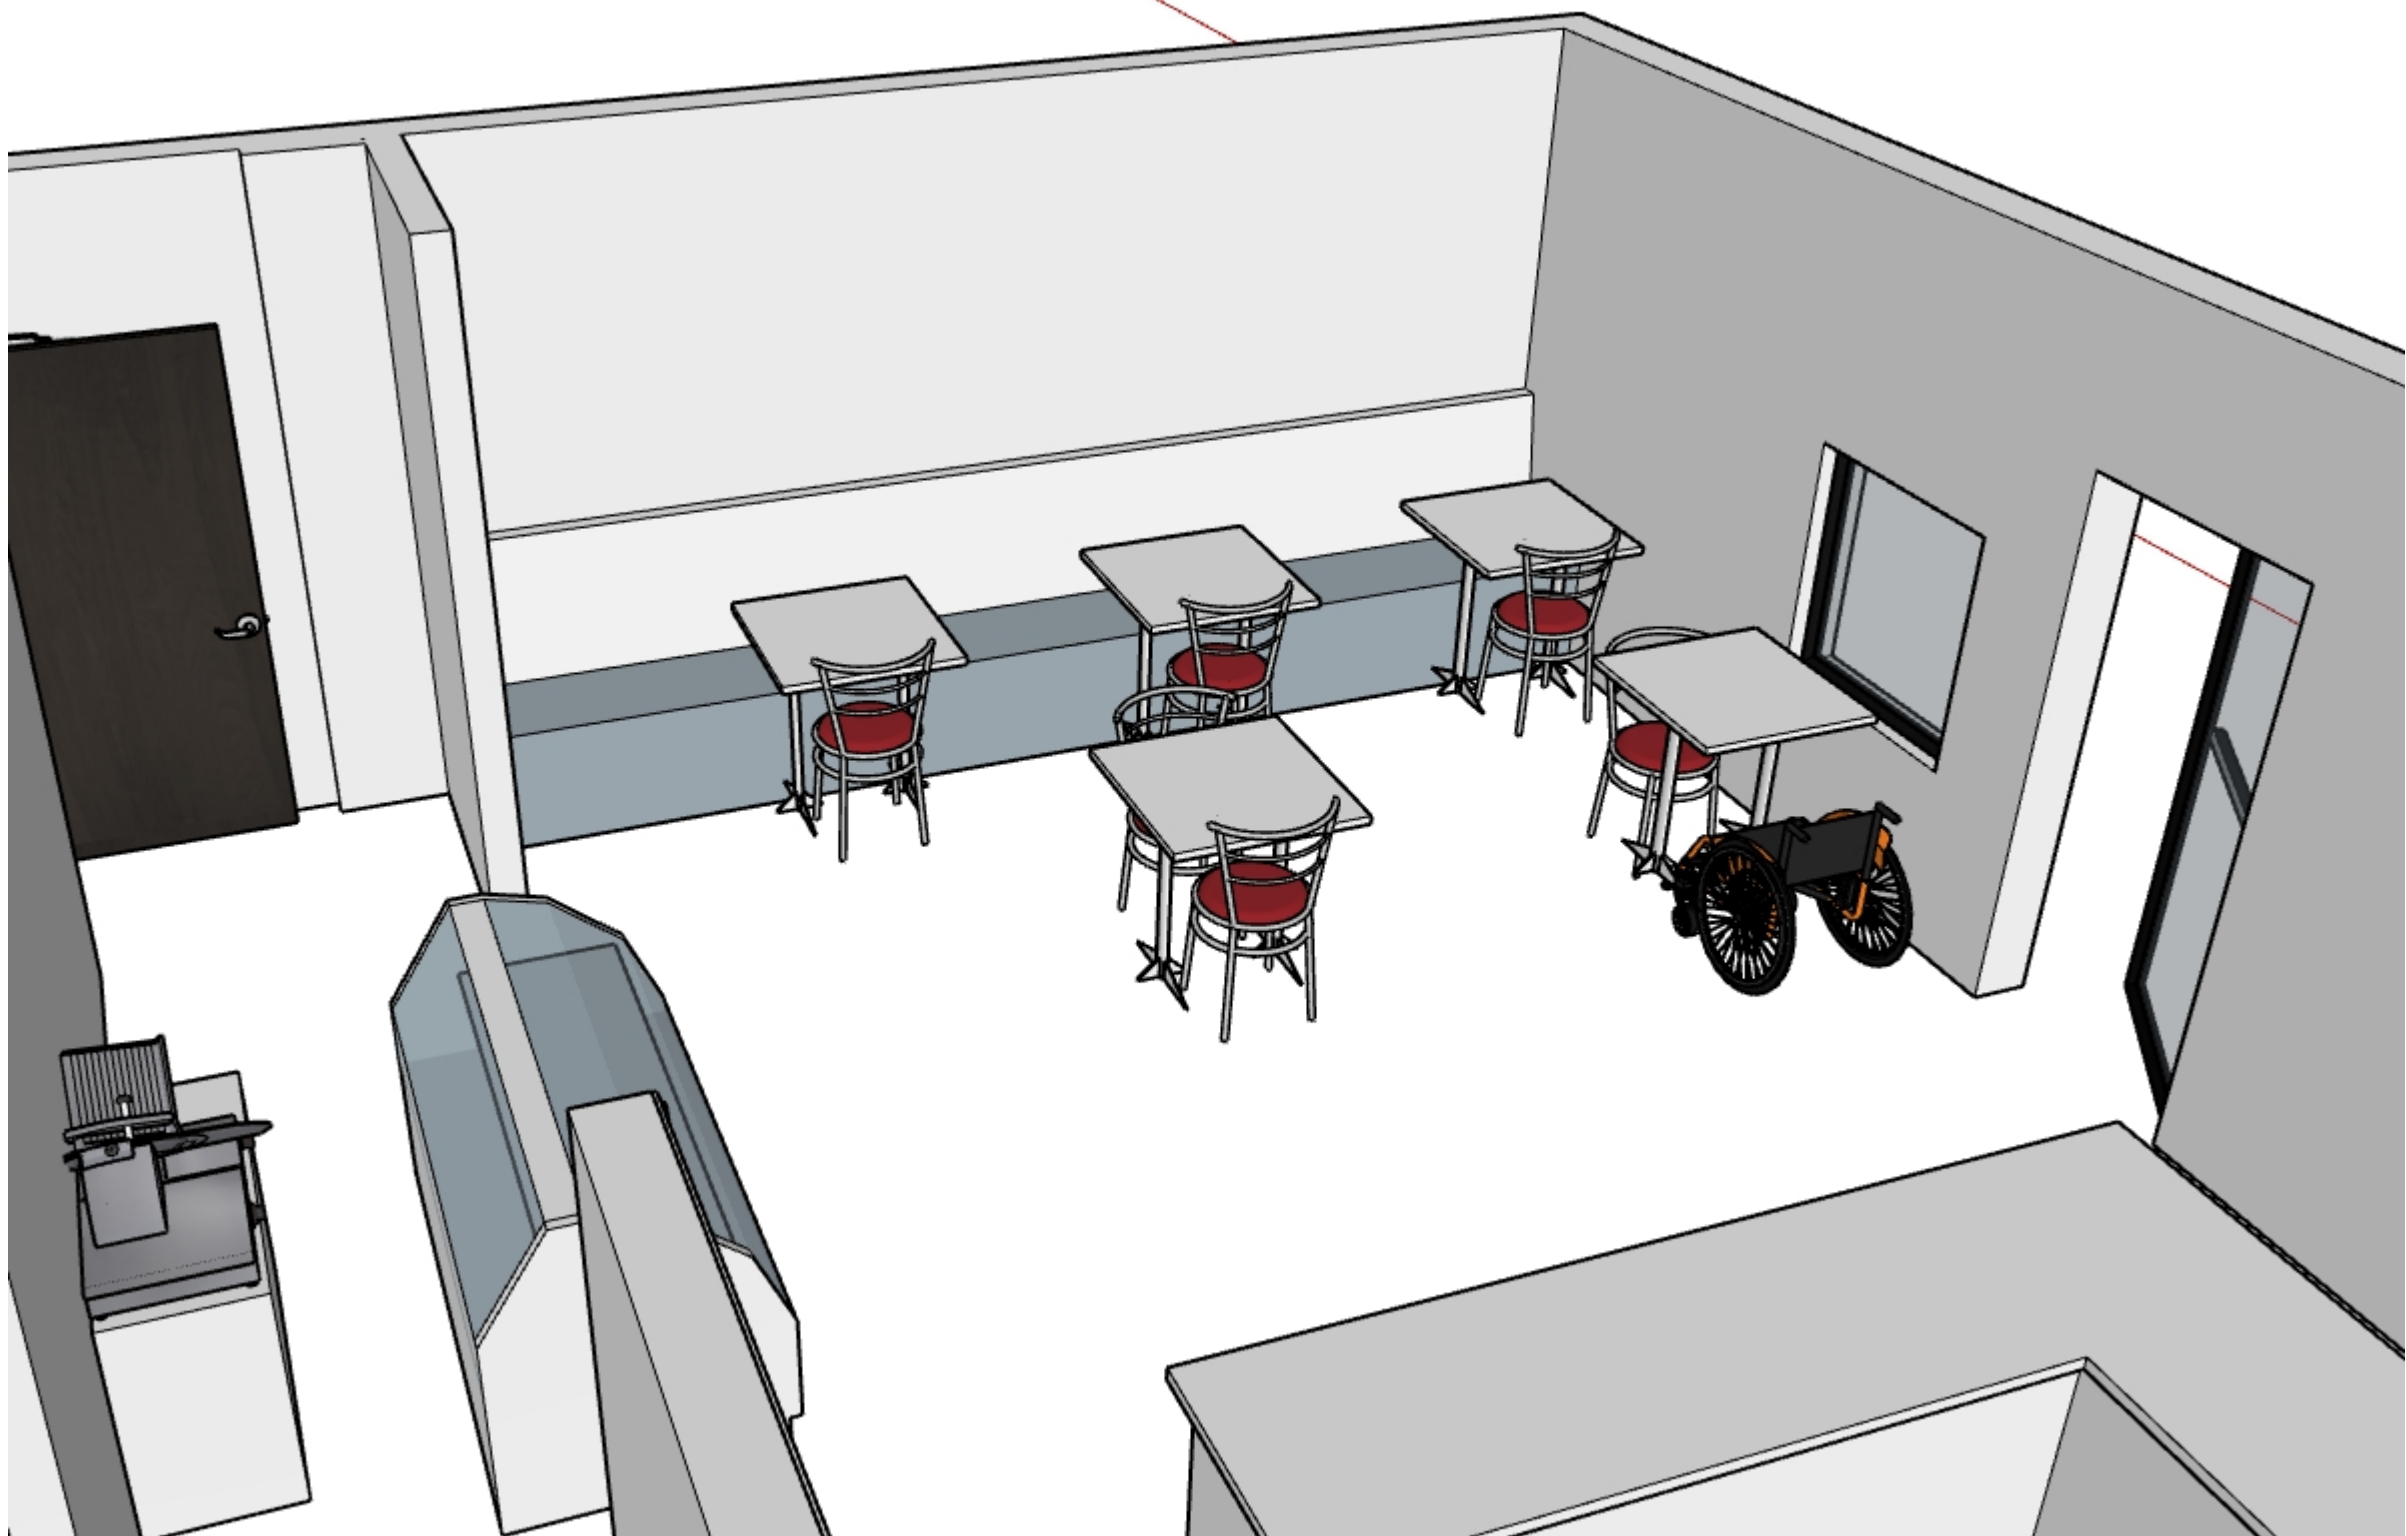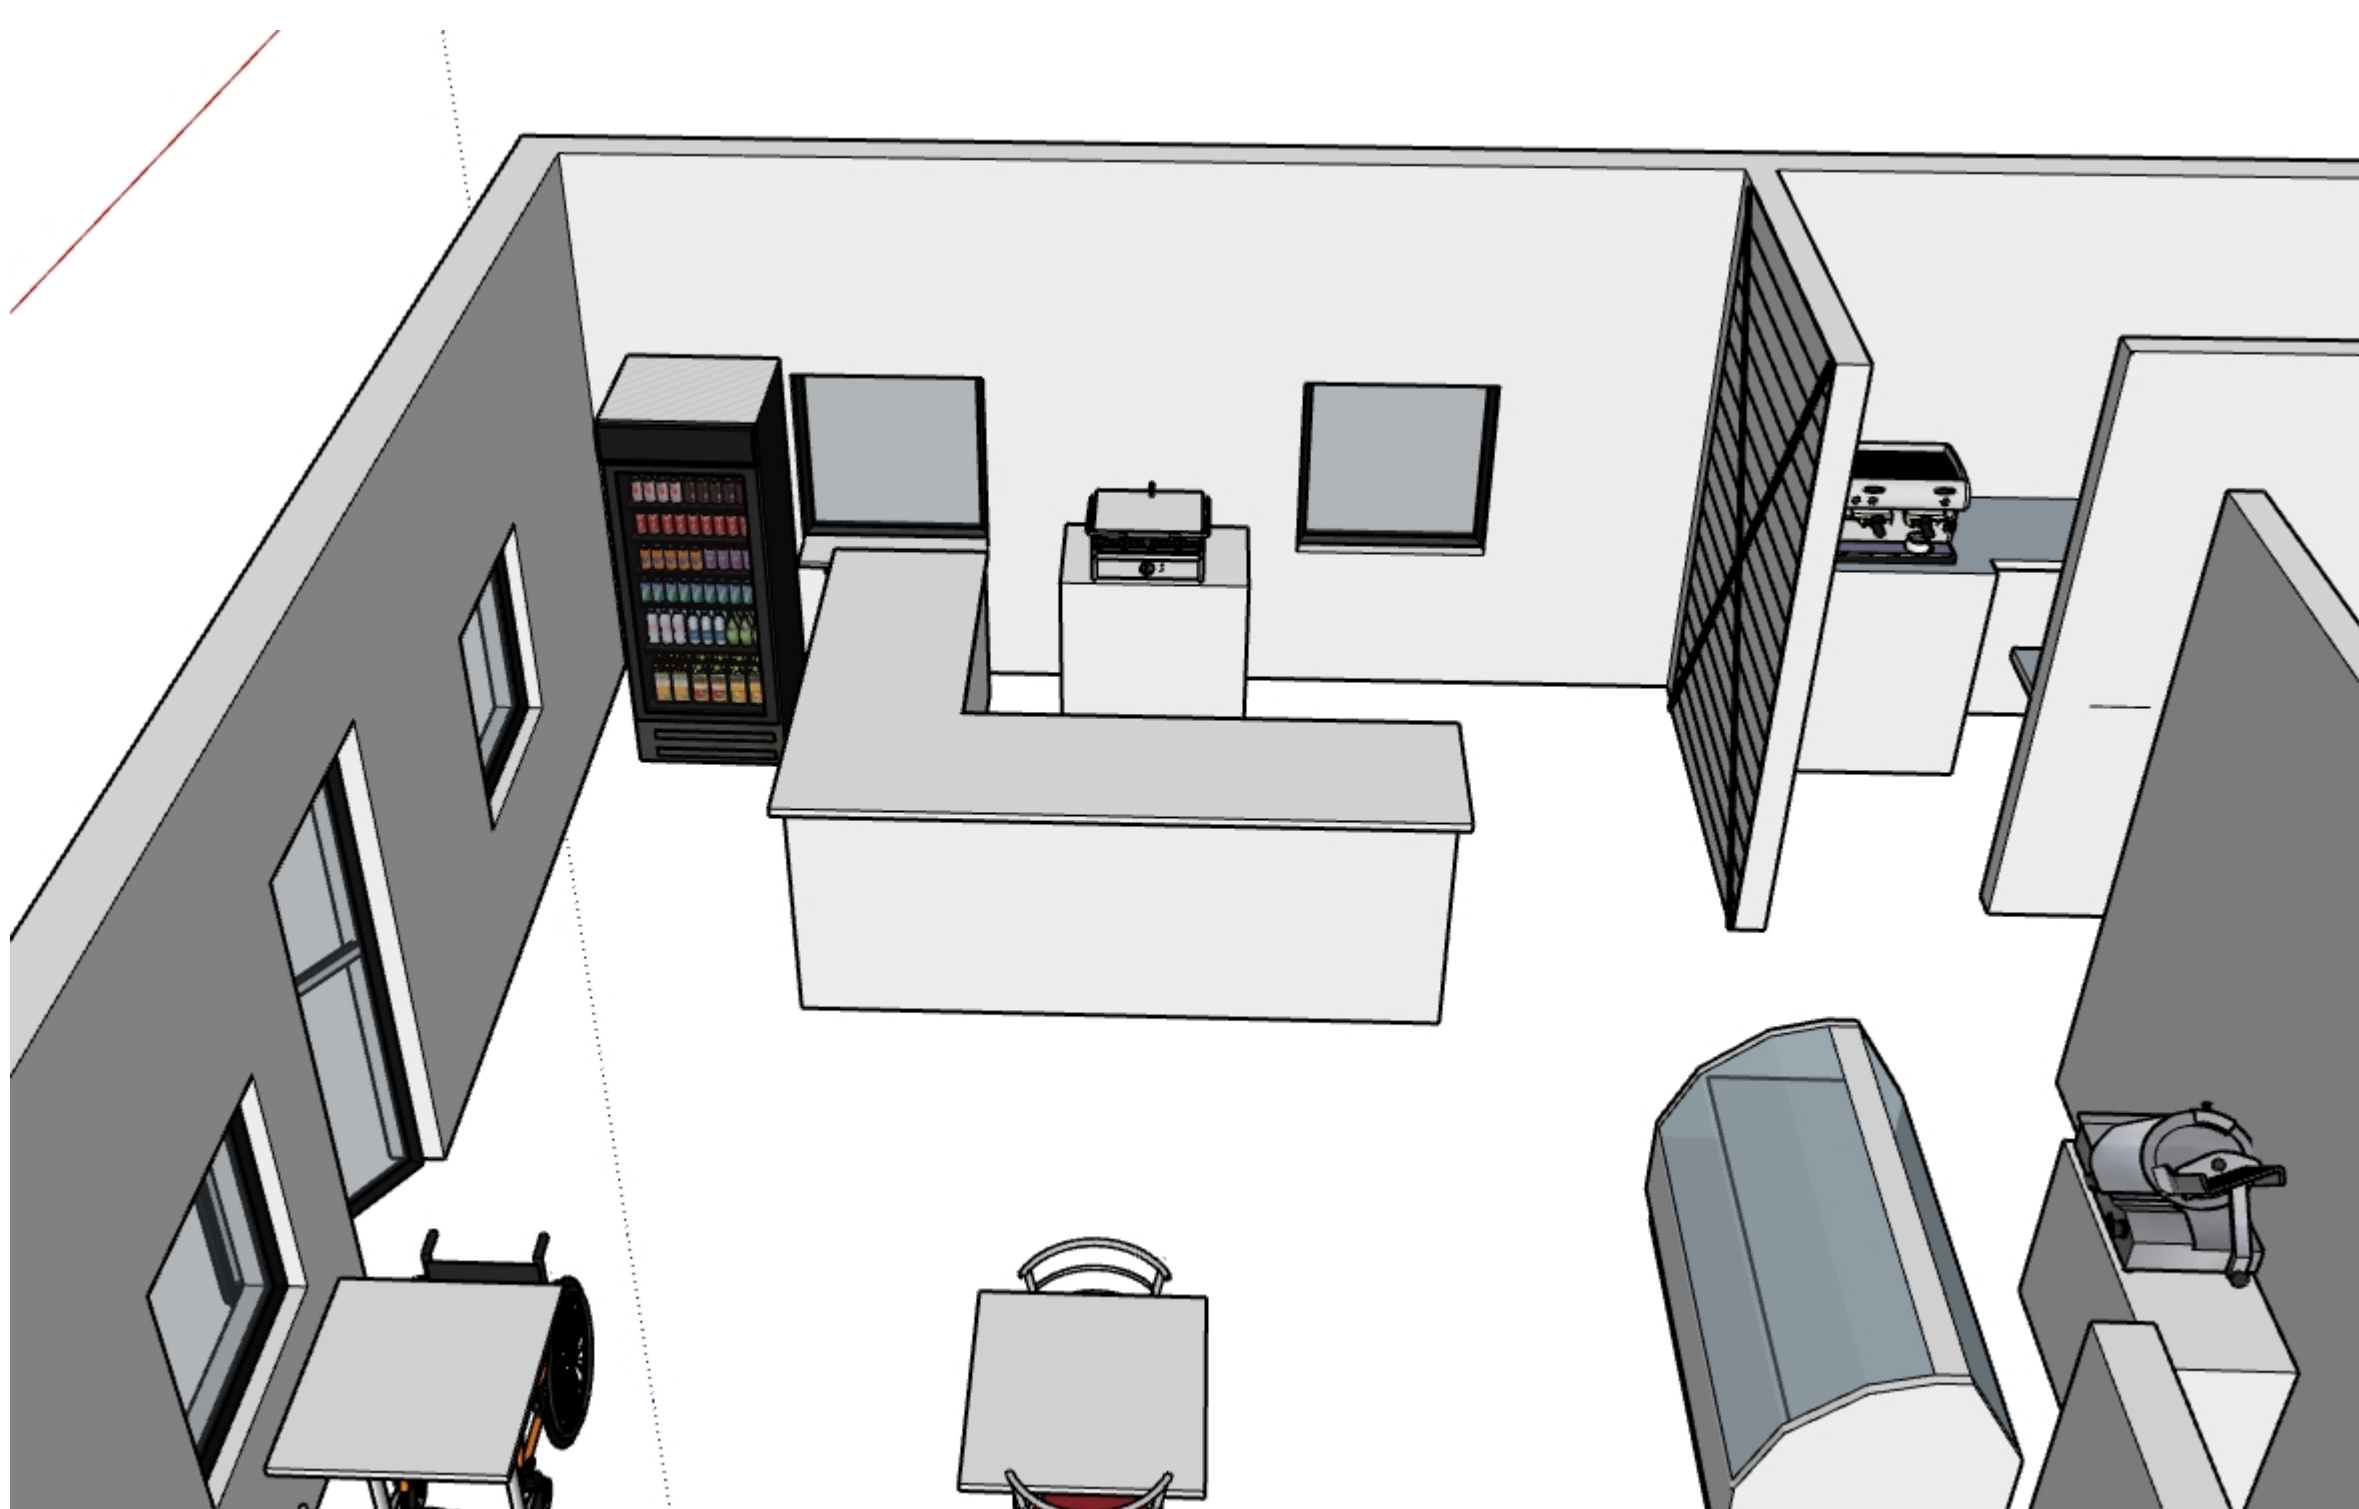

This drawings are sole property of Seating Constructors USA, (DBA Smart Choice Contractors USA) Unless otherwise provided for by contract, or the writing means, the contents of this drawing are confidential & shall be not transmitted to any other party accepted and agreed by Smart Choice Contractors USA. 2025 Copyright .

SHEET TITLE		CUSTOMER NAME:		CUSTOMER INFORMATION		REVISIONS	
ISO DETAILS		AL ABBADESSA		Email: HAROLDCABRERAUSA@GM Phone:AIL.COM3527103932		DRAWINGS LATEST REMARKS	
		PROJECT ADDRESS:		PROJECT OPEN DATE:			
		3429 DELTONA BLVD SPRING HILL, FL. 34606		JUN. 10. 2026			
		PROJECT REVISED BY :		PROJECT REVISED BY :		PROJECT NUMBER: 0024696	
		MICHAEL D. JOHNSON		MICHAEL D. JOHNSON		DESIGN DATE: 01.07.26	