

DISEÑO PROPUESTO
PLANO DE PISO

NOTAS GENERALES DEL PROYECTO – CONVERSIÓN DE
GARAJE A APARTAMENTO TIPO EFFICIENCY

1. DETALLE DE CLÓSET Y ALMACENAMIENTO

CLÓSET INTERIOR DE 12'-0" DE LARGO X 26" DE PROFUNDIDAD INTERIOR, CON DOS PUERTAS CENTRALES DE 30" CADA UNA Y GABINETES LATERALES PARA ALMACENAMIENTO. ÁREA DE PISO APROXIMADA: 26 PIES². CAPACIDAD INTERIOR APROXIMADA: 208 PIES³, CONSIDERANDO UNA ALTURA DE 8'-0".

2. CALENTADOR DE AGUA Y SISTEMA DE FILTRACIÓN

EL CALENTADOR DE AGUA SERÁ INSTALADO DENTRO DEL ÁREA DEL CLÓSET SEGÚN SE MUESTRA EN LOS PLANOS. LA INSTALACIÓN INCLUIRÁ UN SISTEMA DE FILTRACIÓN DE AGUA EN LA LÍNEA PRINCIPAL PARA REDUCIR LA ACUMULACIÓN DE SEDIMENTOS, MINIMIZAR LA CORROSIÓN Y PROLONGAR LA VIDA ÚTIL DEL CALENTADOR, VÁLVULAS, ACCESORIOS Y COMPONENTES DEL SISTEMA DE PLOMERÍA.

3. REUBICACIÓN DEL SISTEMA DE AIRE ACONDICIONADO

EL EQUIPO MANEJADOR DE AIRE (AIR HANDLER) EXISTENTE SERÁ REMOVIDO DE SU UBICACIÓN ACTUAL Y REUBICADO EN EL ÁTICO. SE REALIZARÁ LA RECONEXIÓN COMPLETA DE LOS SISTEMAS ELÉCTRICOS, DE DRENAJE DE CONDENSADOS, DUCTERÍA Y CONTROLES NECESARIOS PARA EL FUNCIONAMIENTO ADECUADO DEL SISTEMA. EL SOPORTE, ACCESO Y PLATAFORMA DEL EQUIPO DEBERÁN CUMPLIR CON EL FLORIDA MECHANICAL CODE 2023.

4. MODIFICACIONES DE PLOMERÍA

EL NUEVO BAÑO HA SIDO UBICADO EN LA ESQUINA INDICADA EN LOS PLANOS PARA OPTIMIZAR LA CONEXIÓN AL SISTEMA SÉPTICO EXISTENTE Y REDUCIR LA LONGITUD DE LAS NUEVAS TUBERÍAS SANITARIAS. LAS LÍNEAS DE AGUA FRÍA, AGUA CALIENTE Y EL DESAGÜE DE LA LAVANDERÍA SERÁN REUBICADOS HACIA LA NUEVA ÁREA DE LAVANDERÍA SEGÚN EL DISEÑO PROPUESTO. TODAS LAS INSTALACIONES DEBERÁN CUMPLIR CON EL FLORIDA PLUMBING CODE 2023.

5. ACTUALIZACIÓN DEL PANEL ELÉCTRICO

EL PANEL ELÉCTRICO EXISTENTE SERÁ ACTUALIZADO A UN PANEL EATON DE 200 AMPERIOS CON CAPACIDAD PARA 20 CIRCUITOS. COMO PARTE DE LA REMODELACIÓN SE INSTALARÁN SEIS (6) CIRCUITOS ELÉCTRICOS NUEVOS, INCLUYENDO EL CIRCUITO DEDICADO PARA EL CALENTADOR DE AGUA, Y LOS CIRCUITOS NECESARIOS PARA LA COCINA, BAÑO, LAVANDERÍA Y ÁREAS HABITABLES, DE CONFORMIDAD CON EL NEC 2020 Y FLORIDA ELECTRICAL CODE 2023.

6. MODIFICACIÓN DE APERTURA Y NUEVO HEADER ESTRUCTURAL

SE DEMOLERÁ LA SECCIÓN DE MURO INDICADA EN LOS PLANOS PARA LA INSTALACIÓN DE UNA NUEVA APERTURA. SE INSTALARÁ UN NUEVO HEADER ESTRUCTURAL DE ACUERDO CON LOS REQUERIMIENTOS DEL CÓDIGO Y LAS CARGAS EXISTENTES. LOS ESPACIOS LATERALES SERÁN RELLENADOS CON CONCRETO Y/O MAMPOSTERÍA PARA LOGRAR UNA TERMINACIÓN UNIFORME Y ADECUADA INTEGRACIÓN CON LA ESTRUCTURA EXISTENTE.

7. PISOS INTERIORES

TODAS LAS ÁREAS INTERIORES HABITABLES RECIBIRÁN PISO TIPO LVP (LUXURY VINYL PLANK) RESISTENTE A LA HUMEDAD, IMPACTOS Y DESGASTE NORMAL. EL COLOR Y ACABADO SERÁN SELECCIONADOS POR EL PROPIETARIO. LA INSTALACIÓN SE REALIZARÁ DE ACUERDO CON LAS ESPECIFICACIONES DEL FABRICANTE.

8. CABLEADO DE DATOS Y TELEVISIÓN


SE INSTALARÁ CABLEADO DE DATOS DEDICADO TIPO CAT6 O SUPERIOR HACIA LA UBICACIÓN DEL TELEVISOR PARA PROPORCIONAR CONEXIÓN DE INTERNET DE ALTA VELOCIDAD. TAMBIÉN SE INSTALARÁ CABLEADO COAXIAL PARA SERVICIO DE TELEVISIÓN POR CABLE SEGÚN LOS REQUERIMIENTOS DEL PROPIETARIO.

9. AISLAMIENTO TÉRMICO Y EFICIENCIA ENERGÉTICA

LAS PAREDES Y TECHOS DEL ÁREA CONVERTIDA SERÁN AISLADOS DE ACUERDO CON EL FLORIDA ENERGY CONSERVATION CODE 2023. SE INSTALARÁ UNA BARRERA REFLECTIVA TIPO RADIANT BARRIER O HEAT BARRIER EN EL ÁTICO PARA REDUCIR LA GANANCIA DE CALOR Y MEJORAR LA EFICIENCIA ENERGÉTICA DE LA VIVIENDA.

10. SISTEMA DE MONITOREO ELÉCTRICO

SE INSTALARÁ UN SISTEMA DE MONITOREO ELÉCTRICO TIPO EMPORIA ENERGY O EQUIVALENTE APROBADO PARA PERMITIR EL CONTROL Y MONITOREO DEL CONSUMO ELÉCTRICO DEL NUEVO APARTAMENTO Y DE LA RESIDENCIA PRINCIPAL.

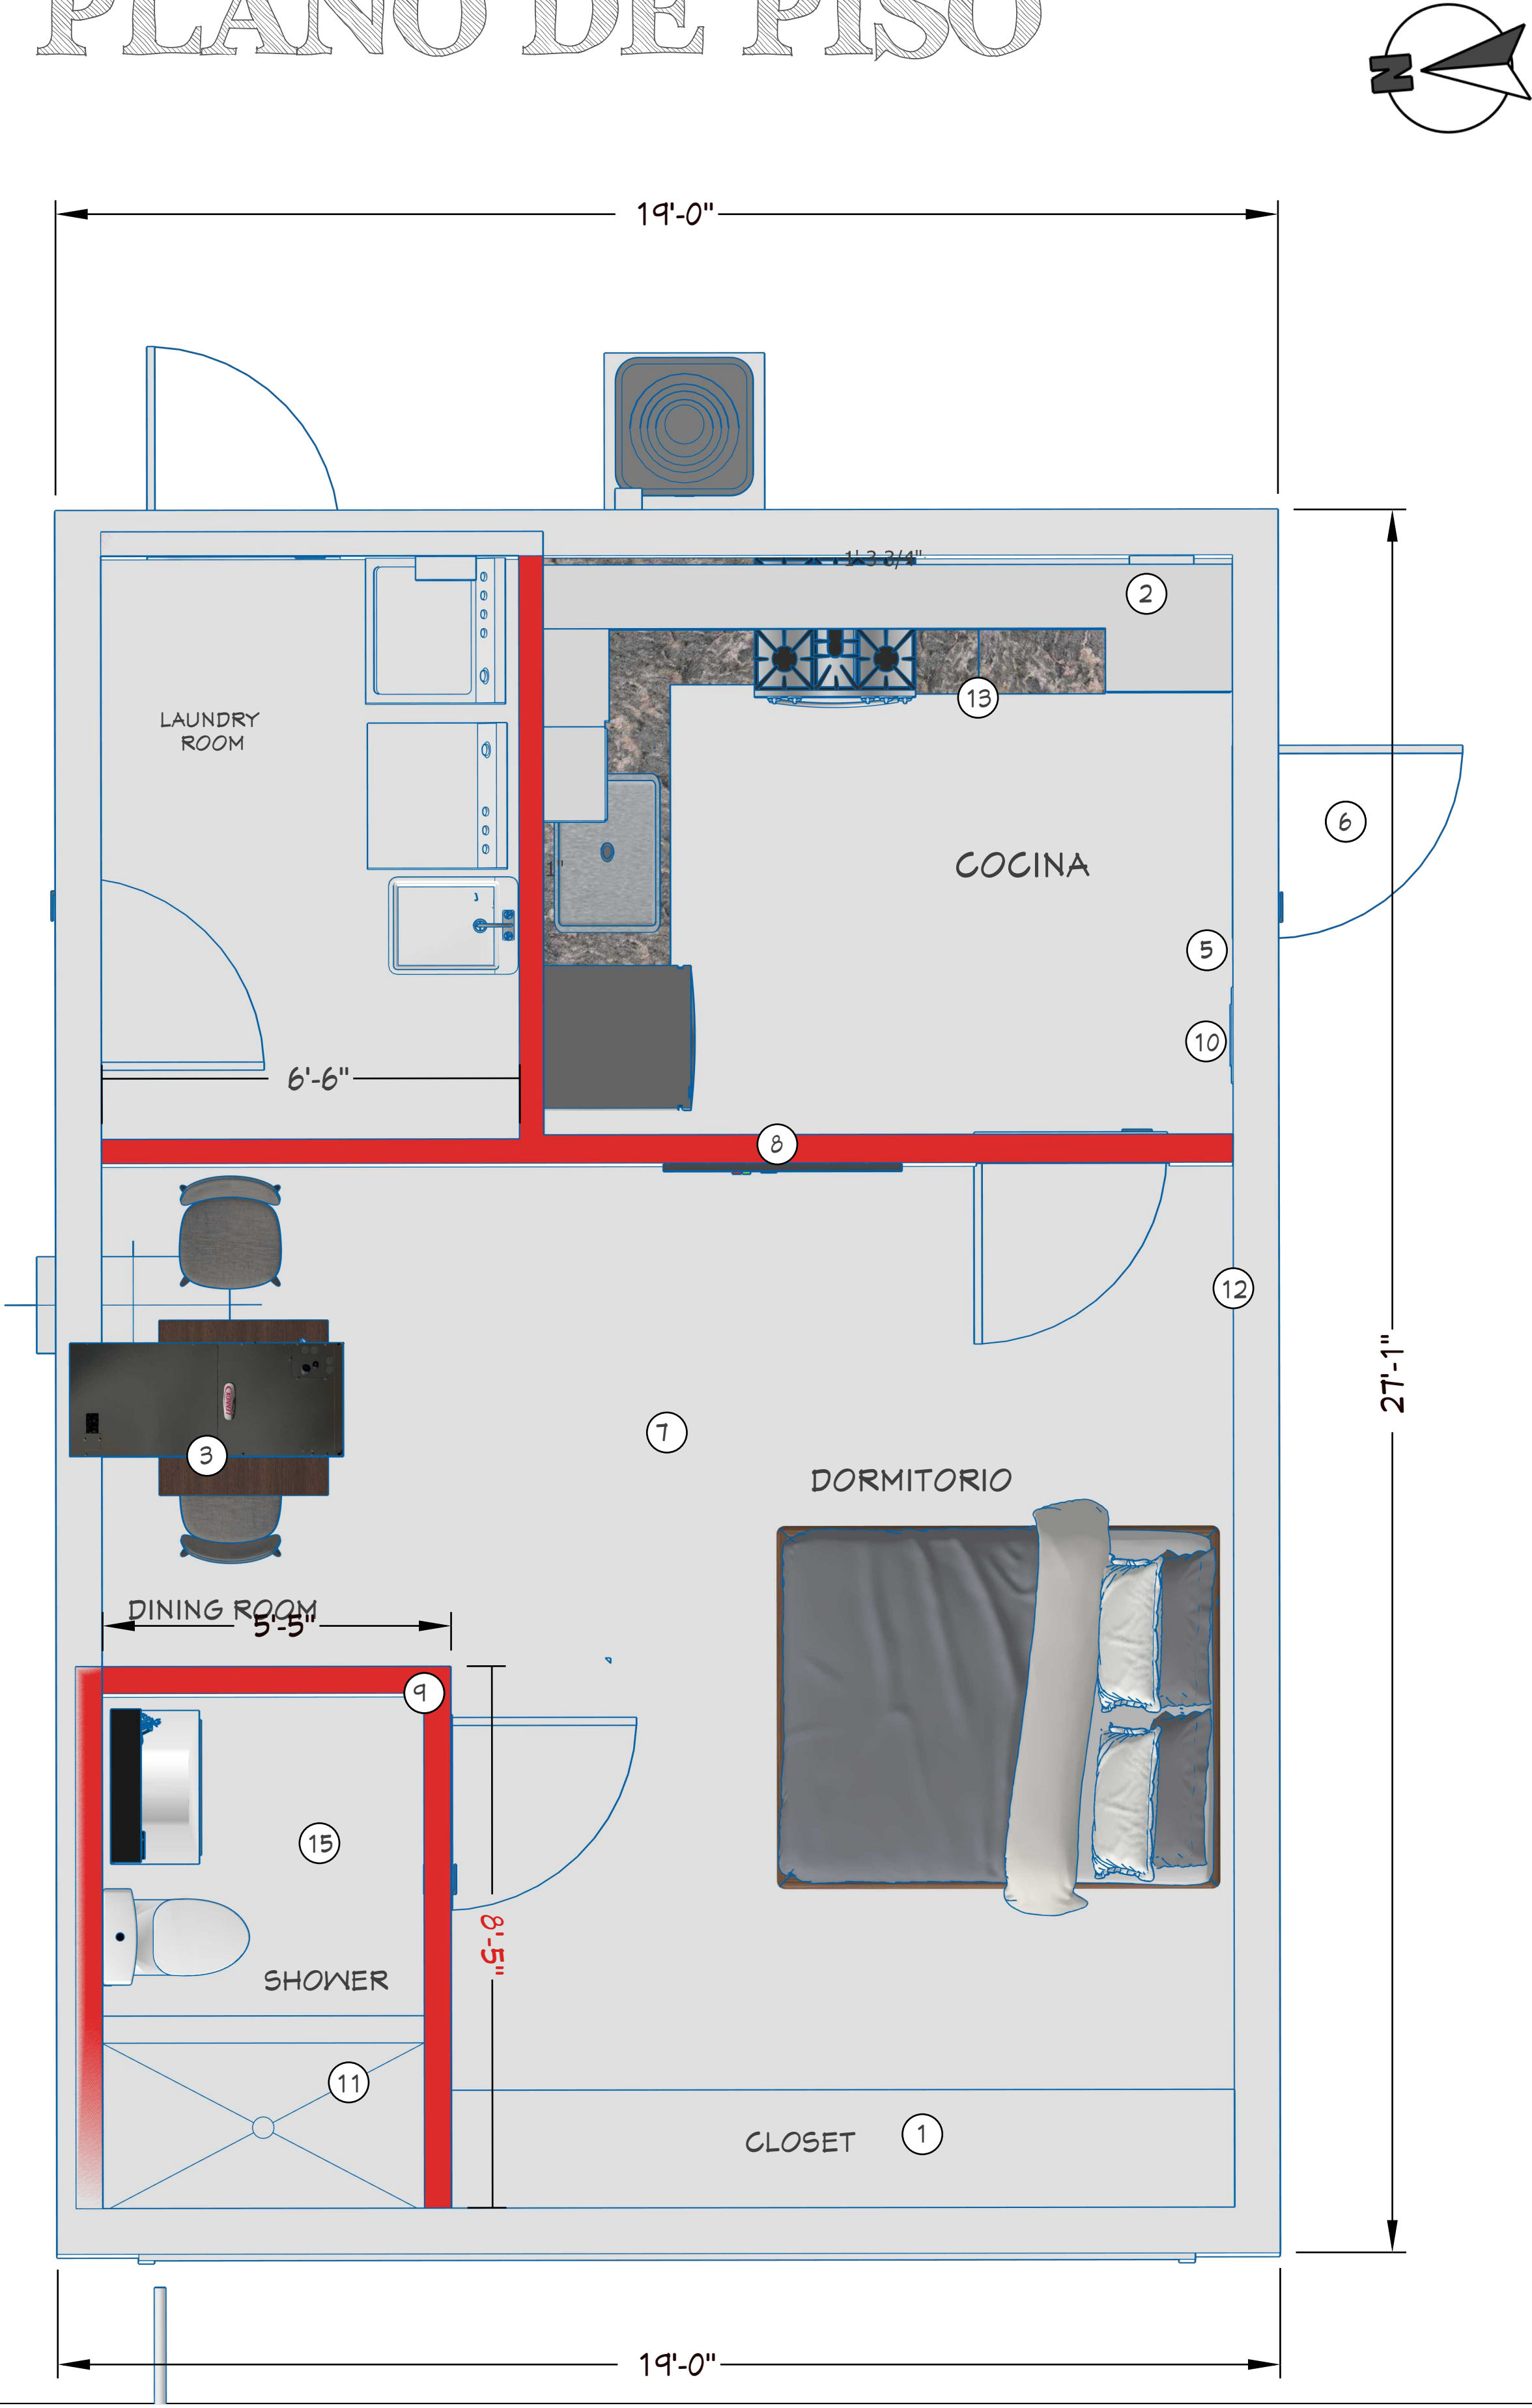

LEYEND:

- EXISTING WALL CMU BLOCK
- EXISTING WALL UMBER NON EXSTRUCTURAL TO BE REMOVED
- EXISTING WINDOWS TO BE REPLACE WITH PLYGEM WINDOWS IMPACT SERIES 400 OR EQUIVELANT
- EXISTING PART OF THE HOUSE NOT BEEN UDTADED OR CHANGES MAKES
- NEW LOCATION FOR THE INSTALLATION OF THE AIR COND. HANDLER ABOVE THE CEALING

11. IMPERMEABILIZACIÓN DEL BAÑO

LAS ÁREAS DE DUCHA Y BAÑO SERÁN IMPERMEABILIZADAS UTILIZANDO MEMBRANA LÍQUIDA TIPO REDGARD O EQUIVALENTE APROBADO. LOS PISOS Y PAREDES DE LAS ÁREAS HÔMEDAS RECIBIRÁN PROTECCIÓN CONTRA FILTRACIONES DE AGUA. LA BASE DE DUCHA INCLUIRÁ LINER IMPERMEABLE INSTALADO SEGÚN EL FLORIDA PLUMBING CODE 2023.

12. ACABADOS DE PINTURA Y TEXTURAS

TODOS LOS CIELOS RASOS SERÁN ACABADOS CON TEXTURA TIPO KNOCKDOWN Y PINTURA FLAT. TODAS LAS PAREDES INTERIORES SERÁN ACABADAS CON TEXTURA TIPO ORANGE PEEL Y PINTURA SATIN DE ALTA DURABILIDAD.

13. GABINETES Y ACCESORIOS

LOS GABINETES DE COCINA, LAVAMANOS, INODOROS, GRIFERÍAS Y DEMÁS ACCESORIOS DE PLOMERÍA SERÁN MARCA AMERICAN STANDARD O EQUIVALENTE APROBADO.

14. DISTRIBUCIÓN DEL SISTEMA DE AIRE ACONDICIONADO

EL NUEVO APARTAMENTO SERÁ CLIMATIZADO MEDIANTE LA EXTENSIÓN DEL SISTEMA CENTRAL EXISTENTE. SE INSTALARÁN CUATRO (4) REGISTROS DE SUMINISTRO DE AIRE ACONDICIONADO UBICADOS EN EL DORMITORIO PRINCIPAL, COCINA, LAVANDERÍA Y BAÑO. TODOS LOS DUCTOS SERÁN INSTALADOS DE ACUERDO CON EL FLORIDA MECHANICAL CODE 2023.

15. VENTILACIÓN MECÁNICA DEL BAÑO

EL BAÑO CONTARÁ CON UN EXTRACTOR MECÁNICO CON DESCARGA DIRECTA AL EXTERIOR, INSTALADO DE ACUERDO CON EL FLORIDA MECHANICAL CODE 2023 Y EL FLORIDA BUILDING CODE RESIDENTIAL 2023.


16. CUMPLIMIENTO DE CÓDIGOS

LA CONSTRUCCIÓN, REMODELACIÓN, INSTALACIÓN DE EQUIPOS, MODIFICACIONES ESTRUCTURALES, ELÉCTRICAS, MECÁNICAS, DE PLOMERÍA Y ACABADOS DESCRITOS EN ESTOS PLANOS DEBERÁN EJECUTARSE DE CONFORMIDAD CON EL FLORIDA BUILDING CODE 2023 (8TH EDITION), FLORIDA RESIDENTIAL CODE 2023, FLORIDA ELECTRICAL CODE BASADO EN NEC 2020, FLORIDA PLUMBING CODE 2023, FLORIDA MECHANICAL CODE 2023, FLORIDA ENERGY CONSERVATION CODE 2023 Y TODAS LAS ORDENANZAS Y REQUISITOS APLICABLES DEL CONDADO DE HERNANDO Y DEL ESTADO DE LA FLORIDA.

17. DESCARGO DE RESPONSABILIDAD

TODAS LAS DIMENSIONES, UBICACIONES, CONDICIONES EXISTENTES Y ELEMENTOS ESTRUCTURALES DEBERÁN SER VERIFICADOS EN CAMPO ANTES DEL INICIO DE LOS TRABAJOS. CUALQUIER DISCREPANCIA ENTRE LOS PLANOS Y LAS CONDICIONES EXISTENTES DEBERÁ SER NOTIFICADA AL DISEÑADOR, CONTRATISTA Y AUTORIDAD COMPETENTE ANTES DE PROCEDER CON LA CONSTRUCCIÓN. NINGÚN CONTRATISTA DEBERÁ ESCALAR DIMENSIONES DIRECTAMENTE DE LOS PLANOS

This drawings are sole property of Seating Constructors USA, (DBA Smart Choice Contractors USA) Unless otherwise provided for by contract, or the writing means, the contents of this drawing are confidential & shall be not transmitted to any other party accepted and agreed by Smart Choice Contractors USA. 2025 Copyright.

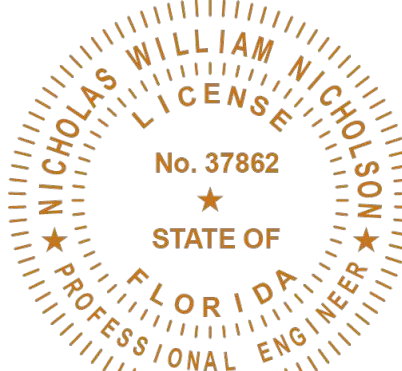SHEET TITLE	CUSTOMER NAME:		CUSTOMER INFORMATION			NICHOLSON ENGINEERING ASSOCIATES, INC.		REVISIONS		A 01	
	HAROLD CABRERA		Email: HAROLDCABRERAUSA@GMAIL.COM Phone: AIL.COM7271553786					DRAWINGS LATEST REMARKS			
	PROJECT ADDRESS:		PROJECT OPEN DATE:					1	01.07.26		RENOVATION DRAWINGS PERMIT SET.
	14689 SW 24TH PLACE OCALA, FL 34560		JAN. 20 2026					2			
FLOOR PLAN			PROJECT REVISED BY : MICHAEL D. JOHNSON								
					PROJECT NUMBER: 0024602		DESIGN DATE: 01.07.26				